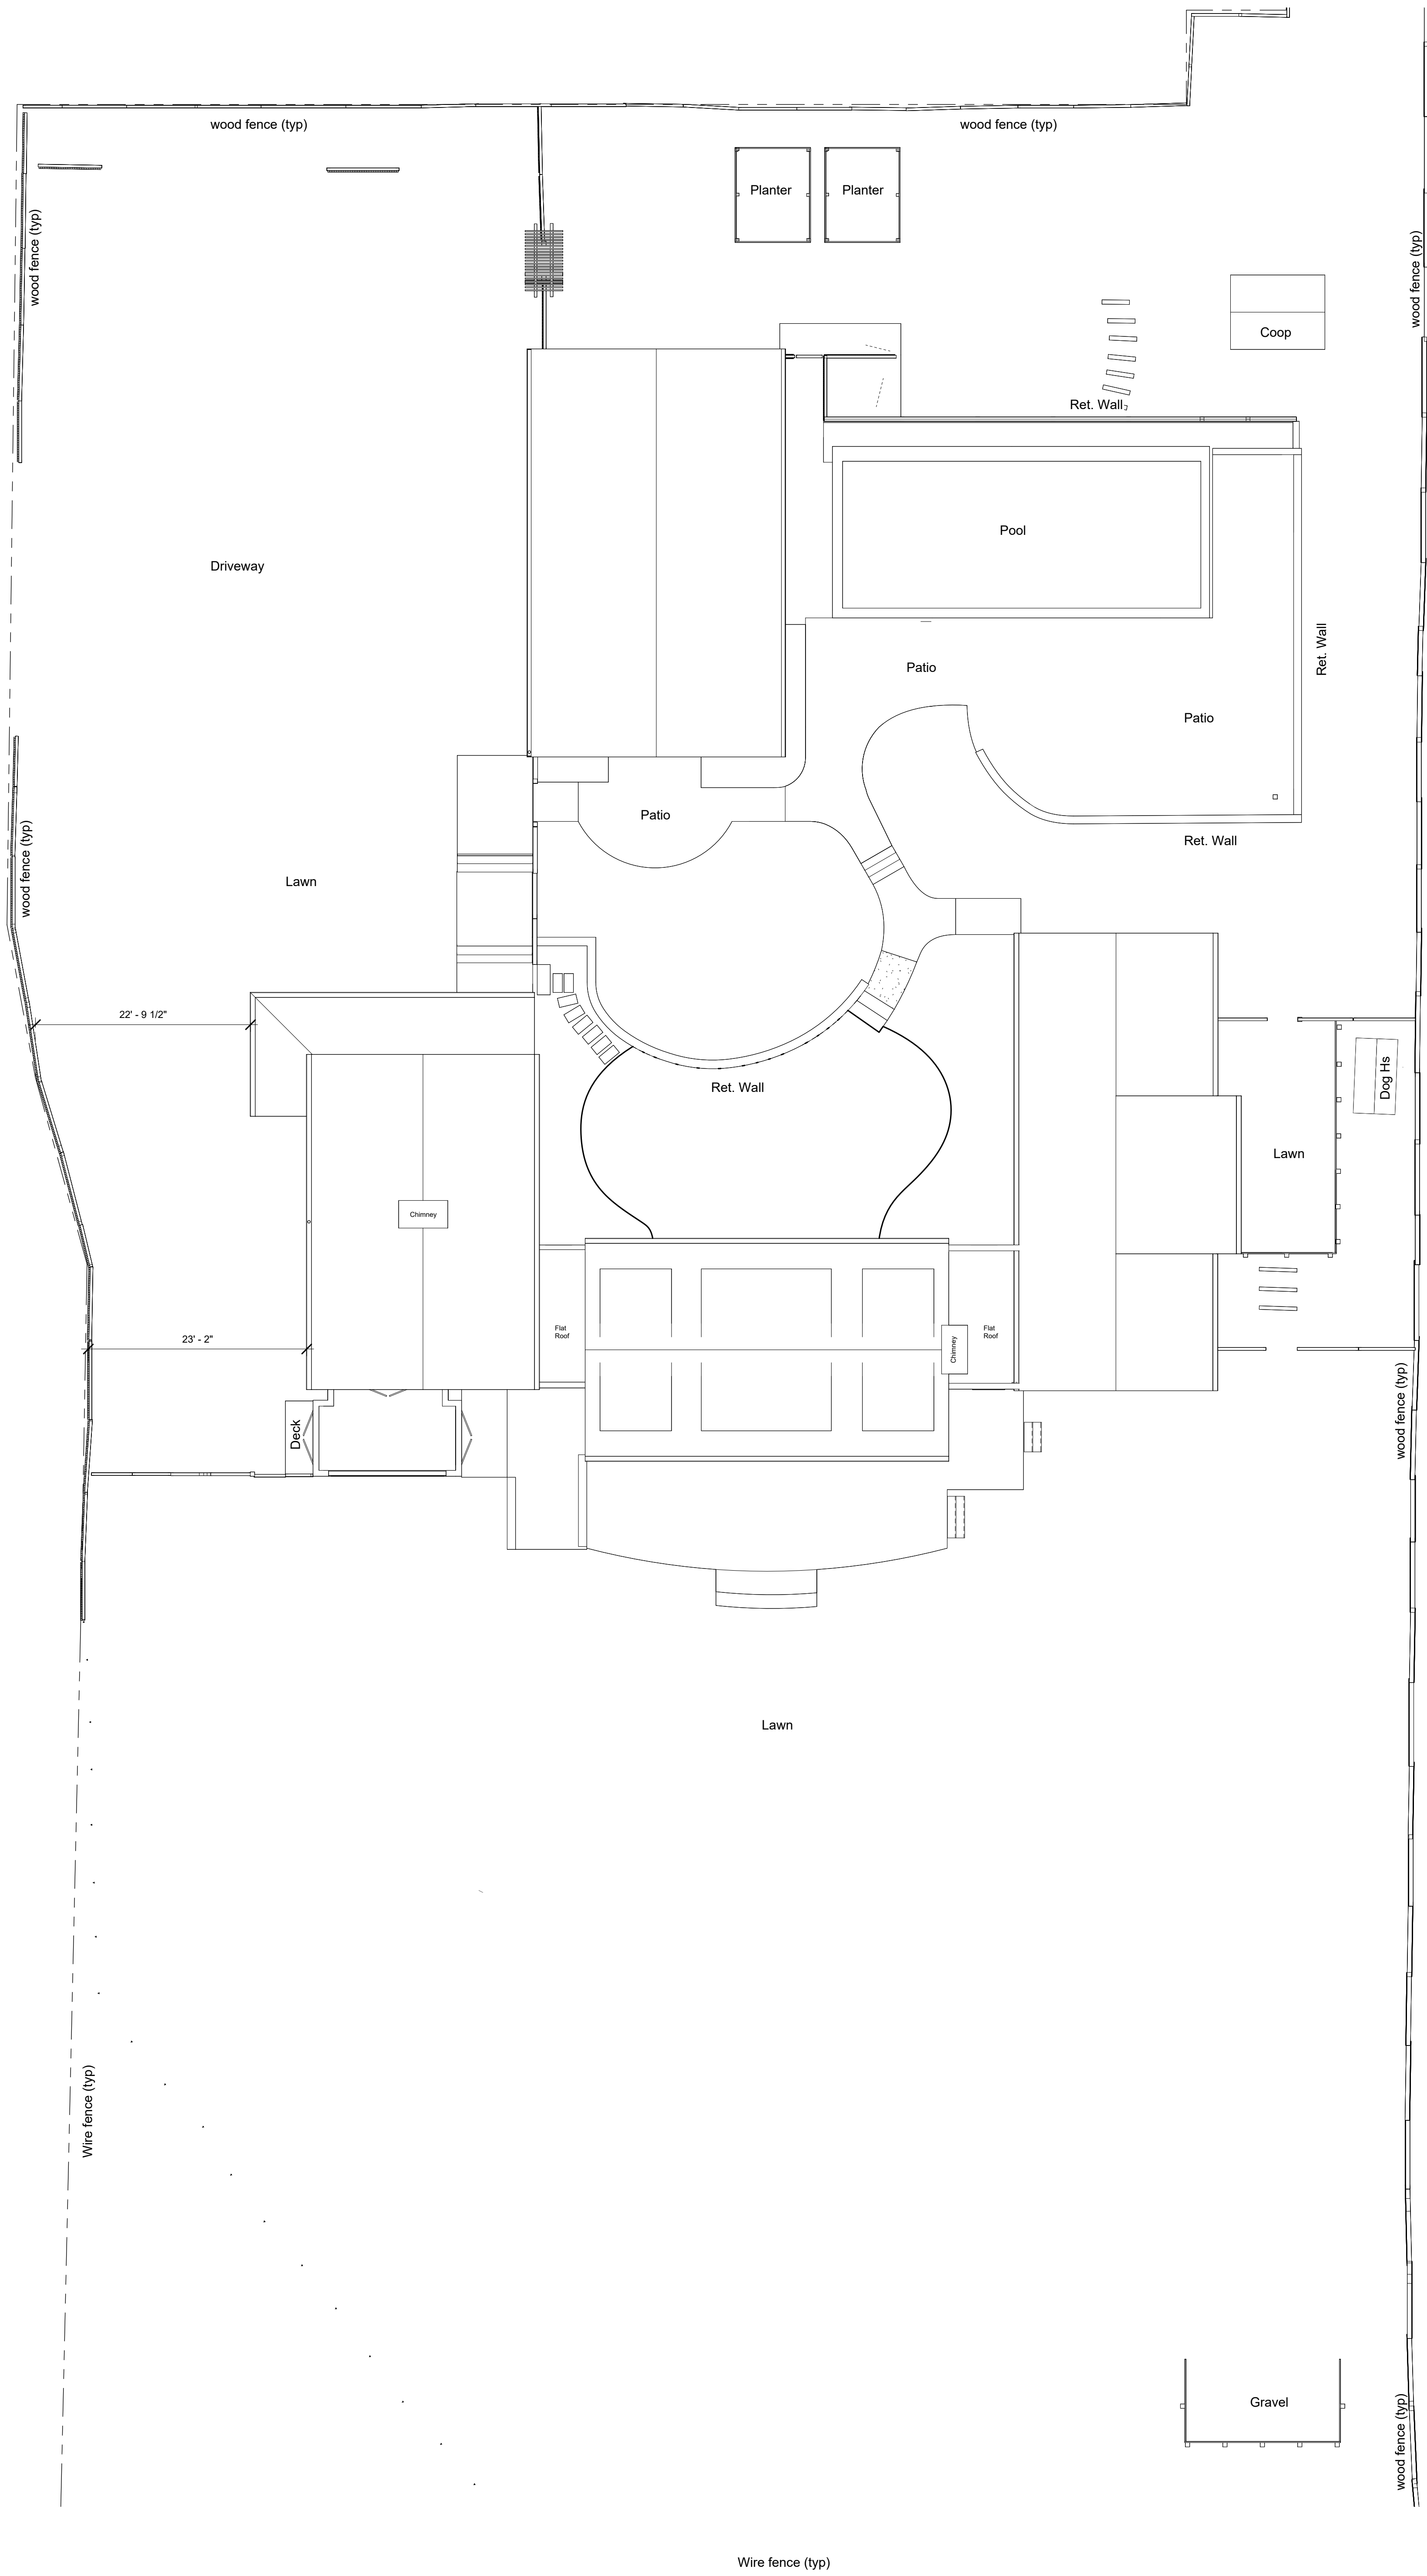


C0.000

XXX

SITE PLAN - EXISTING

Existing Conditions

RESIDENT




Drawn

Author



GROUND TRUTH
CAPTURE REALITY AT SCALE

1 MAIN LEVEL 1 - BASE
1/4" = 1'-0"

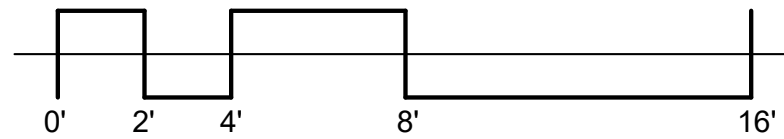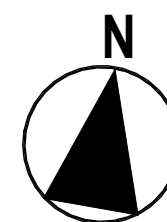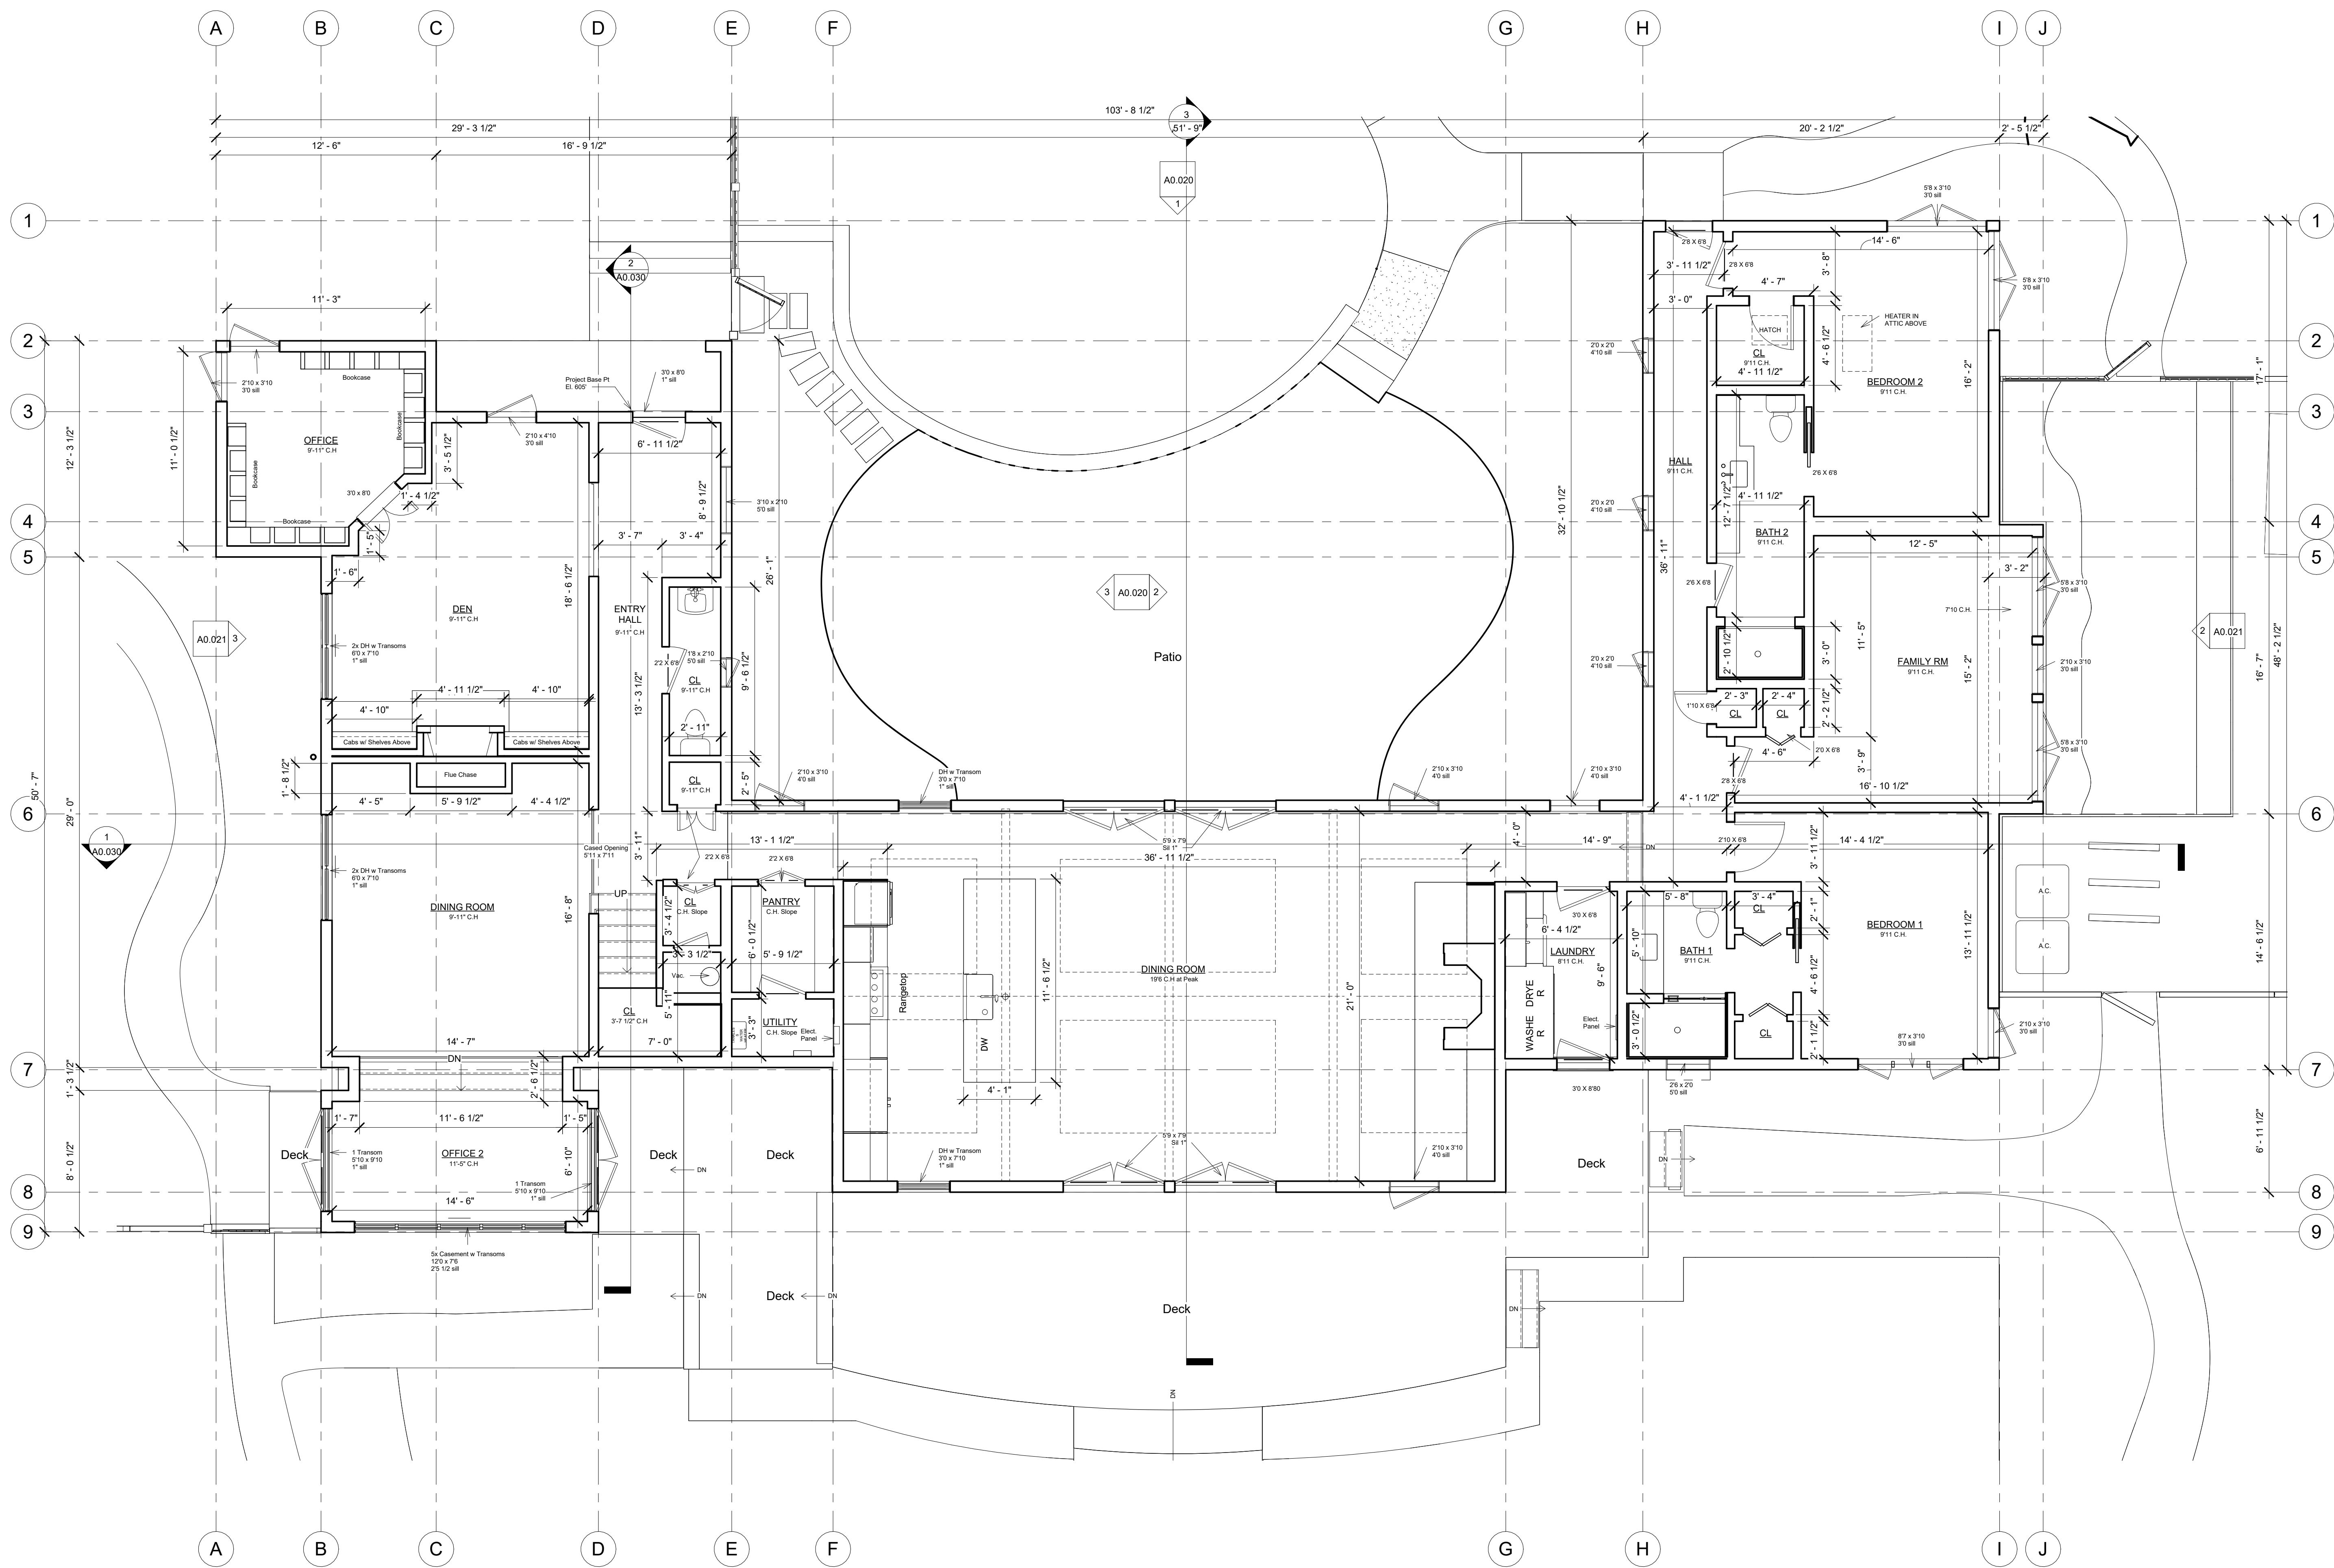

XXX

LEVEL 1 EXISTING CONDITIONS

SHEET NO.

A0.010

Scale 1/4" = 1'-0"

Existing Conditions

RESIDENT




Drawn

Author



GROUND TRUTH
CAPTURE REALITY AT SCALE

1 MAIN LEVEL 2 - BASE
1/4" = 1'-0"

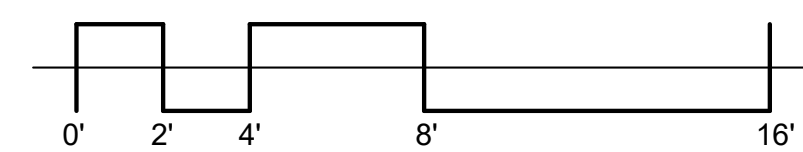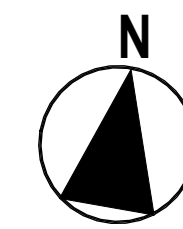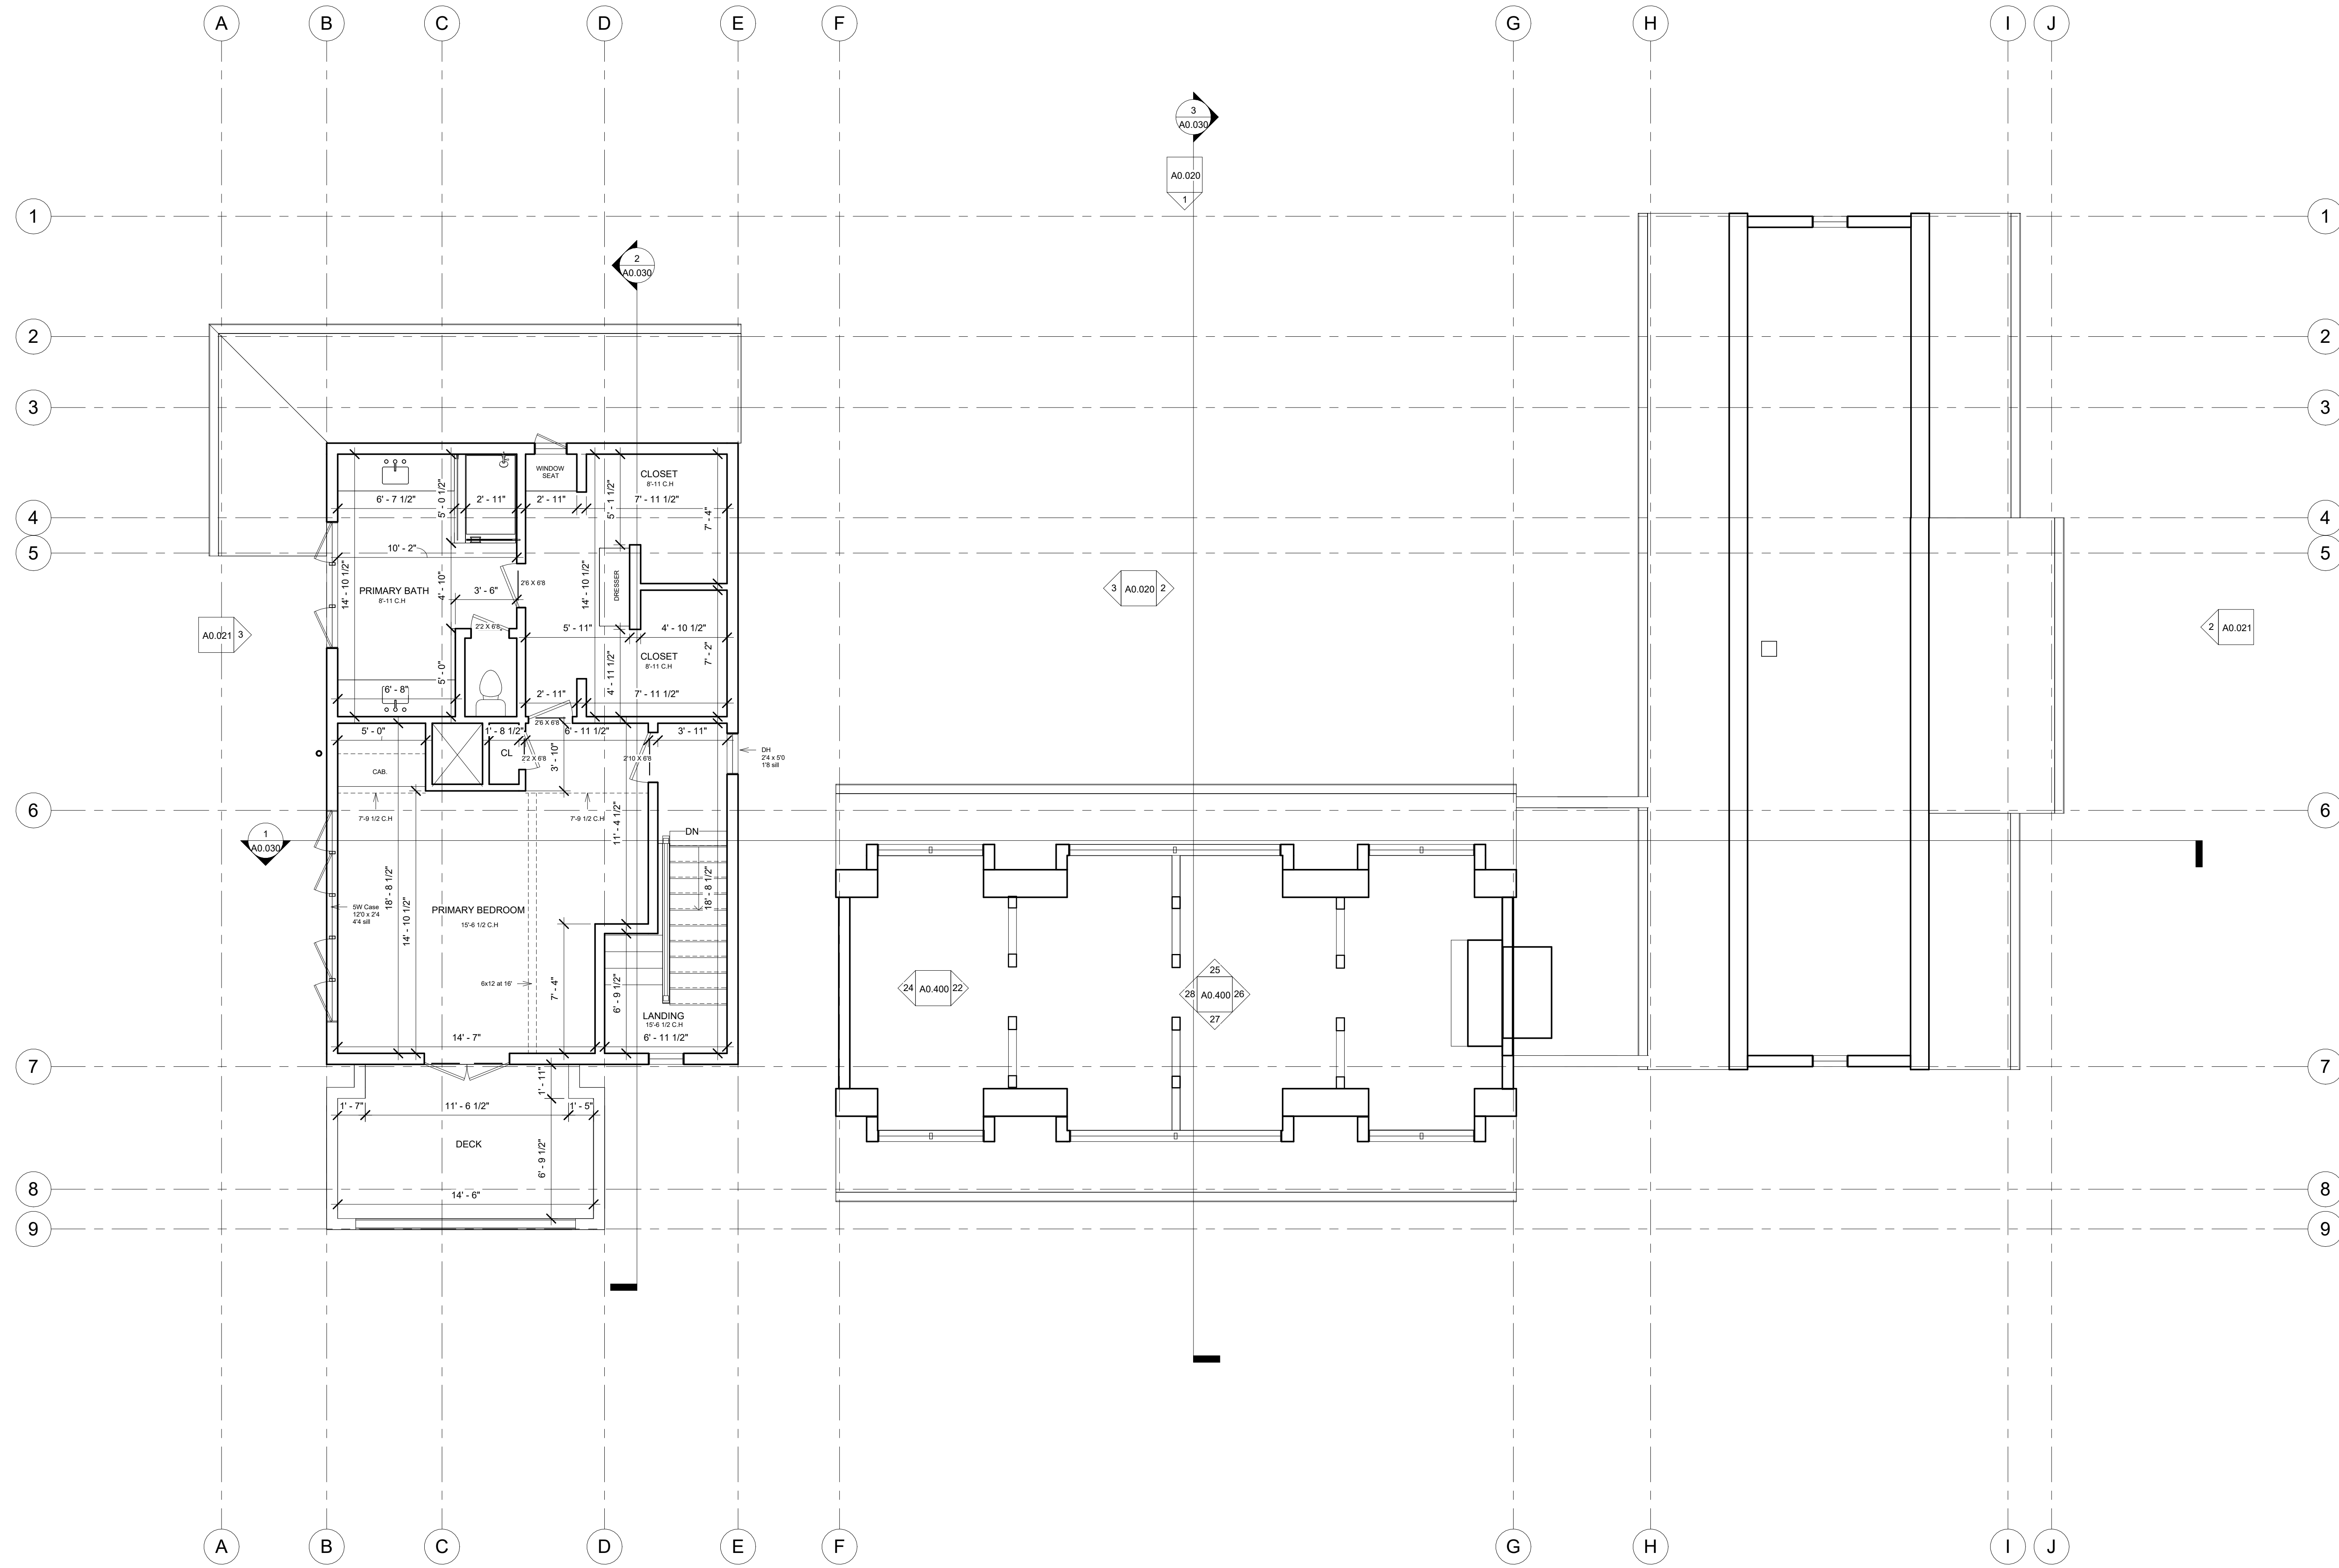

XXX

SHEET NO.

A0.011

Scale 1/4" = 1'-0"

Existing Conditions

LEVEL 2 EXISTING CONDITIONS




RESIDENT

Drawn

Author



GROUND TRUTH
CAPTURE REALITY AT SCALE

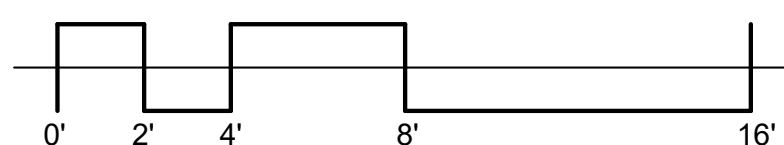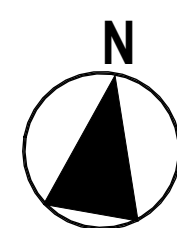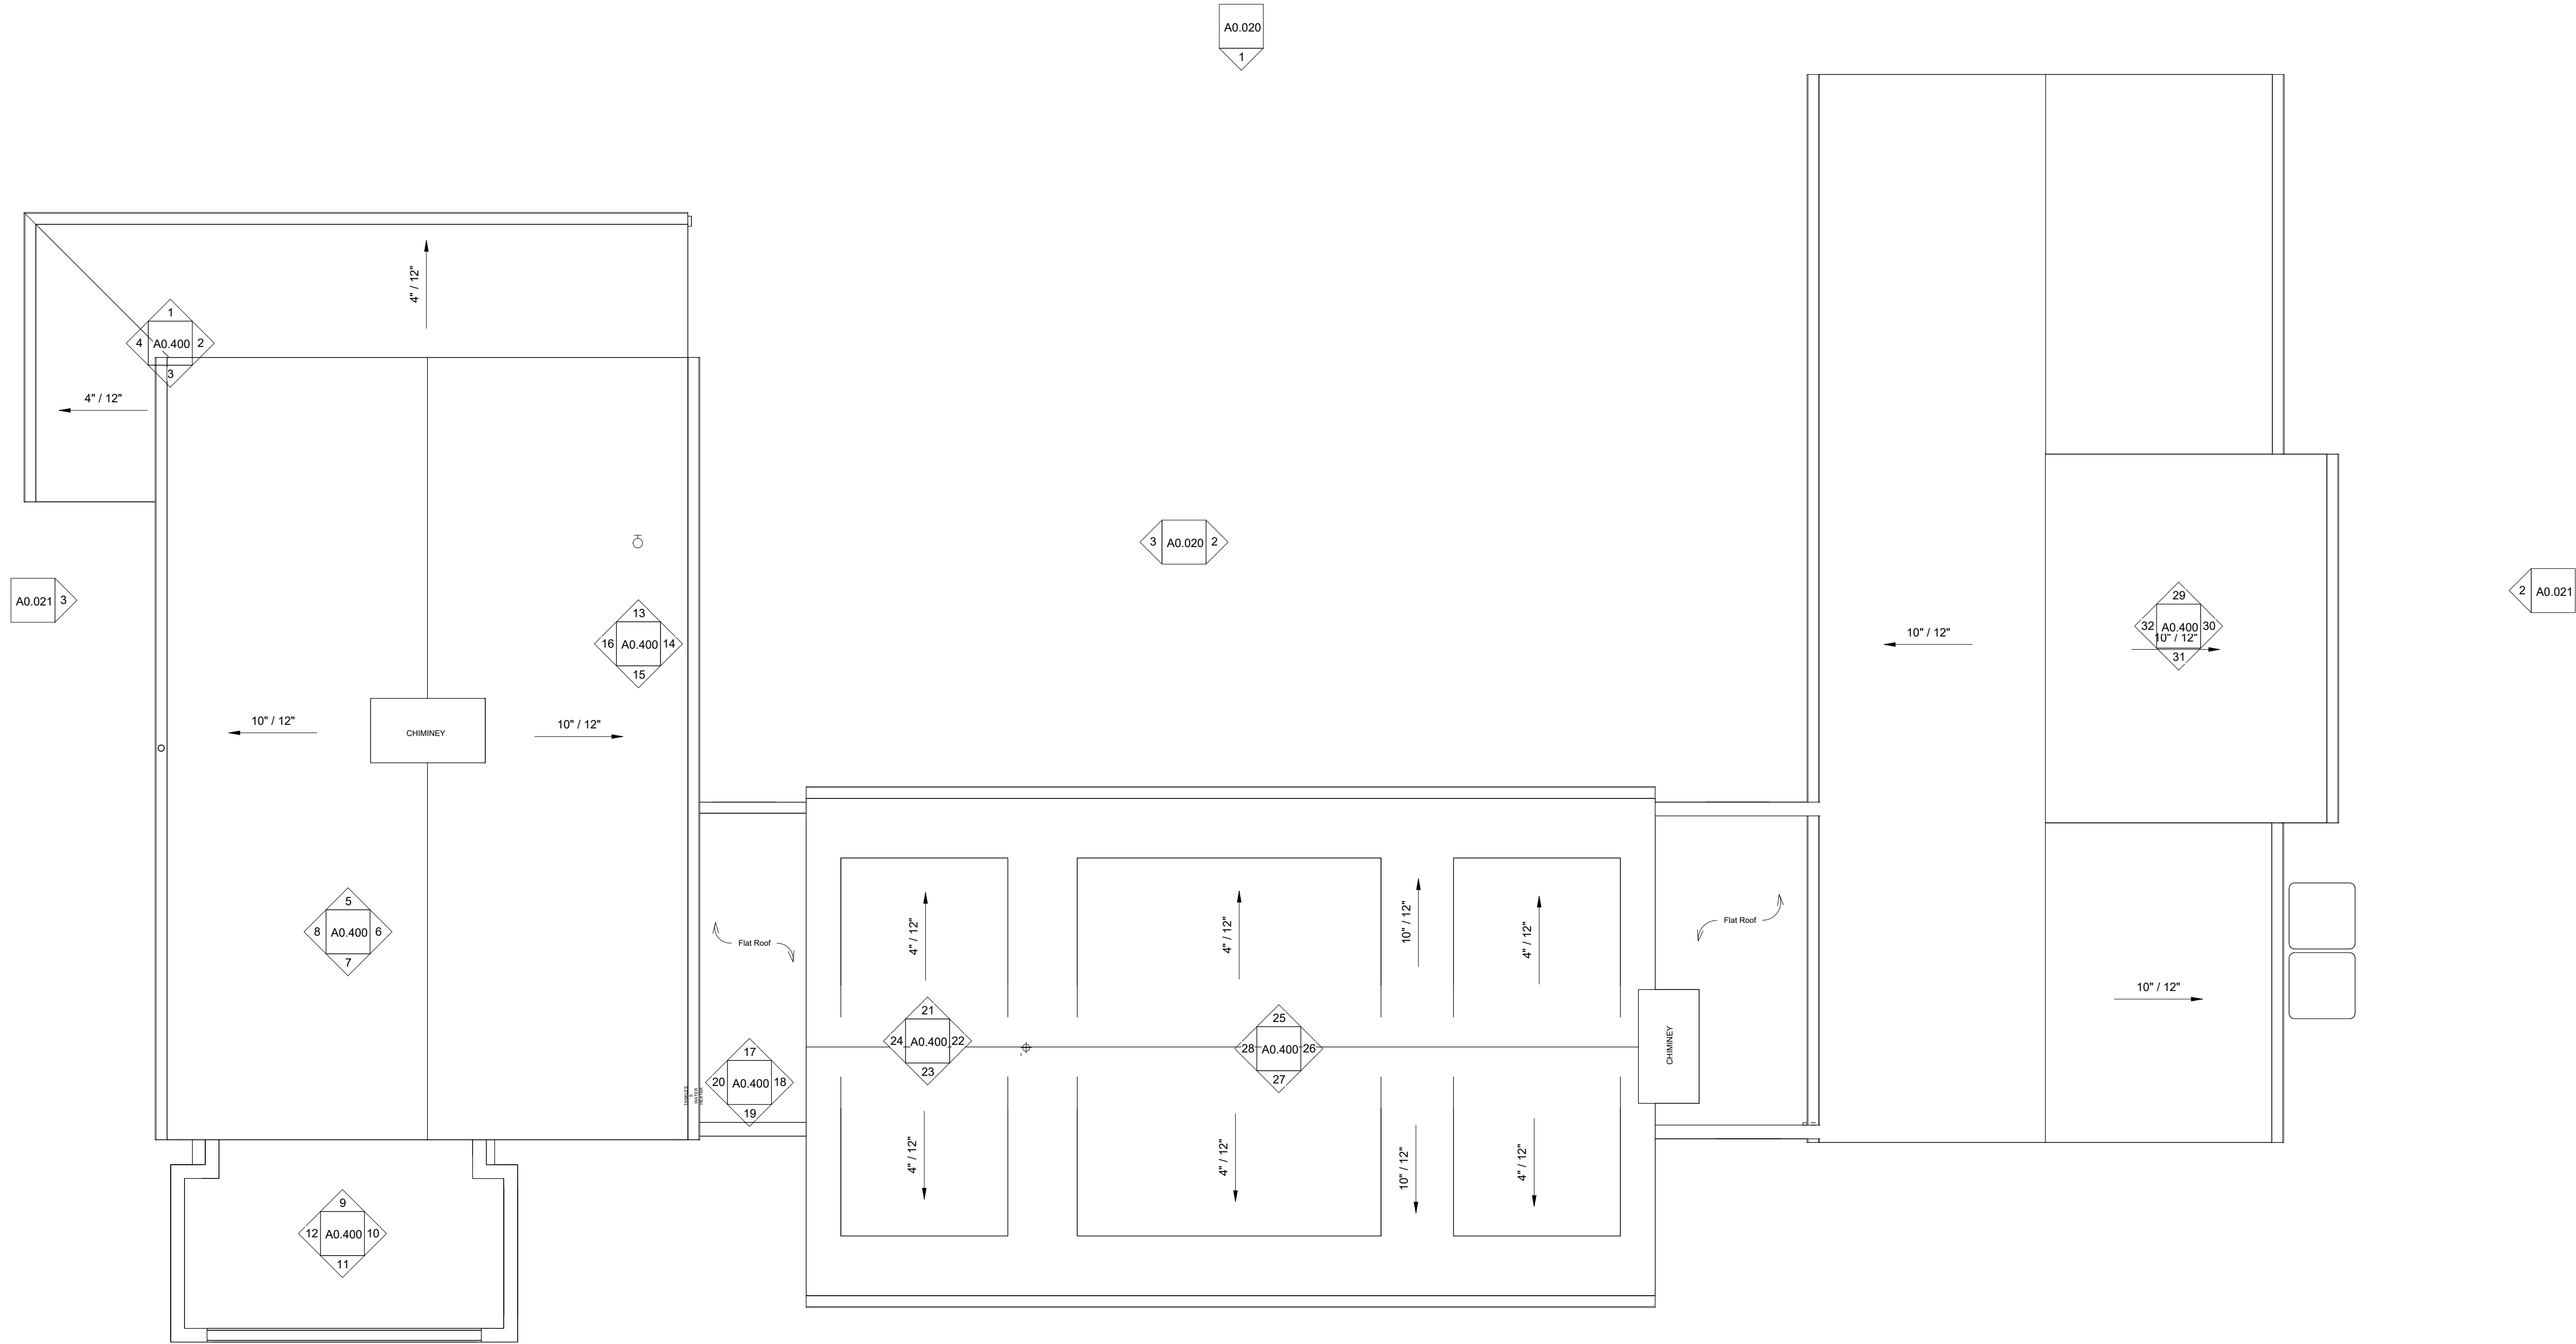

SHEET NO.

A0.012

XXX

ROOF PLAN

Existing Conditions


RESIDENT

Drawn


Author




GROUND TRUTH
CAPTURE REALITY AT SCALE

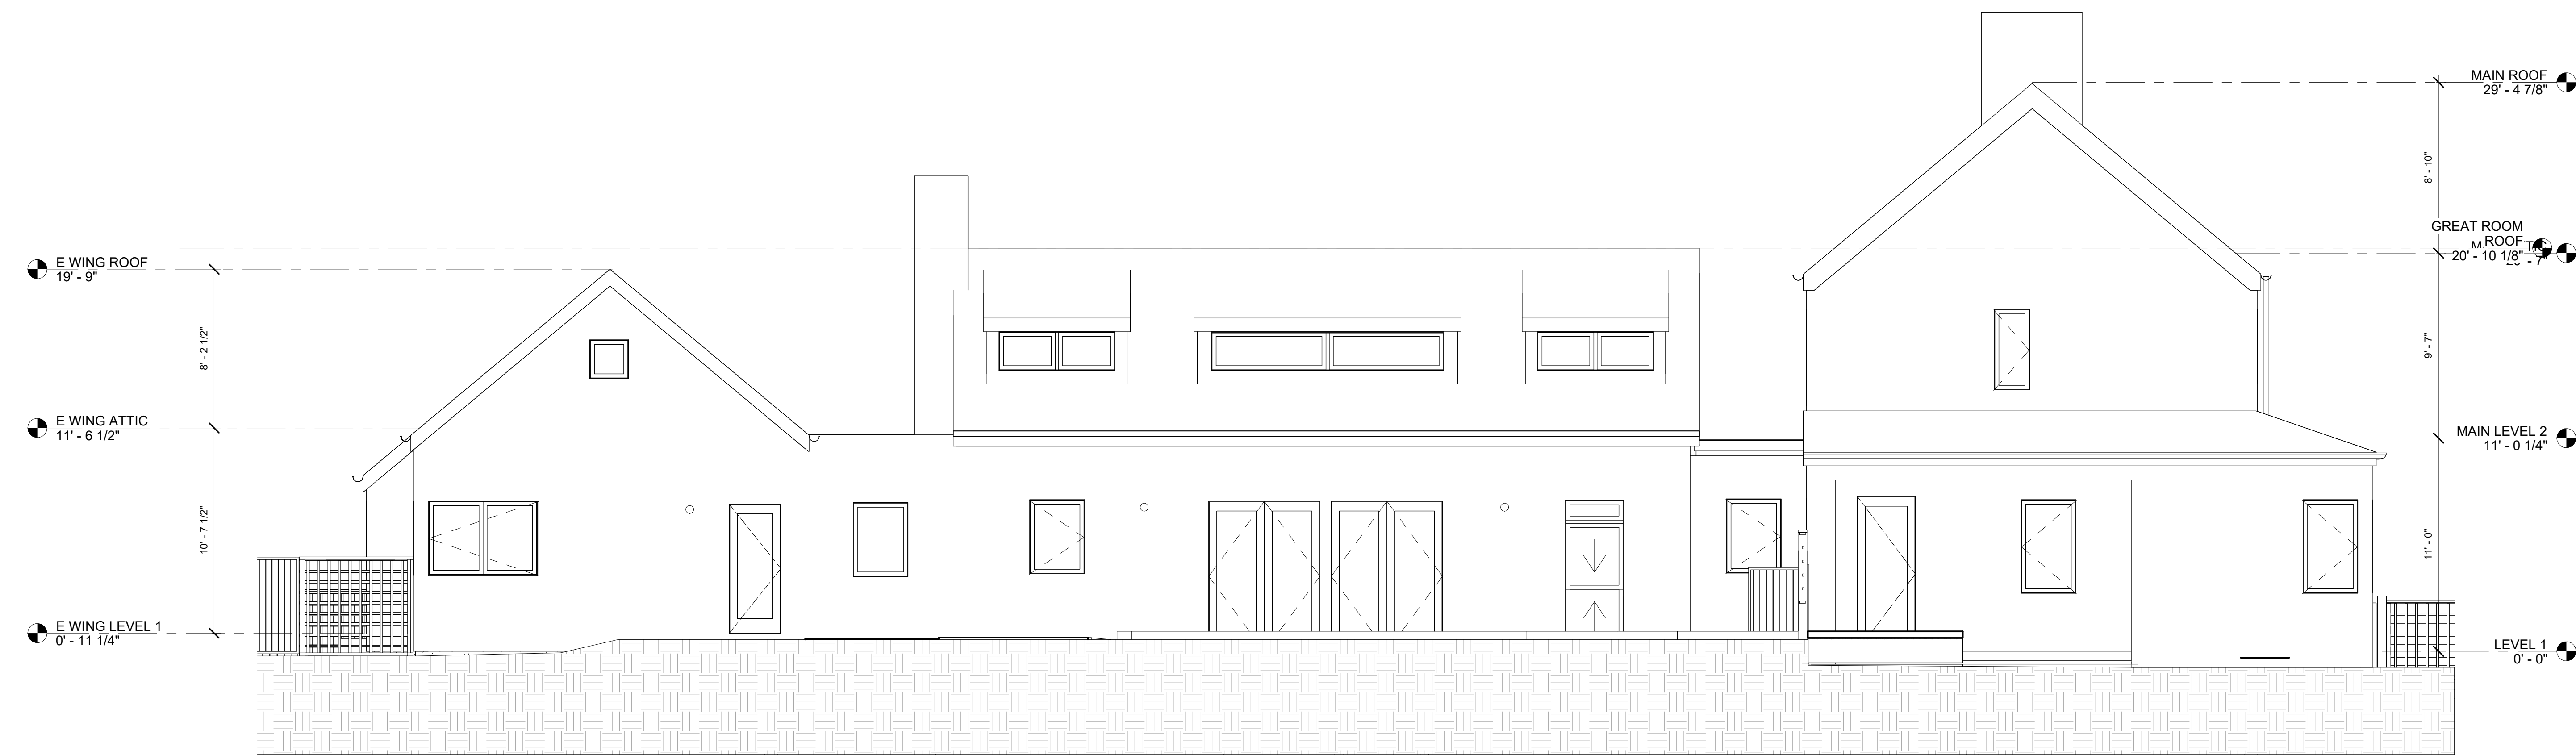

① NORTH ELEVATION
1/4" = 1'-0"

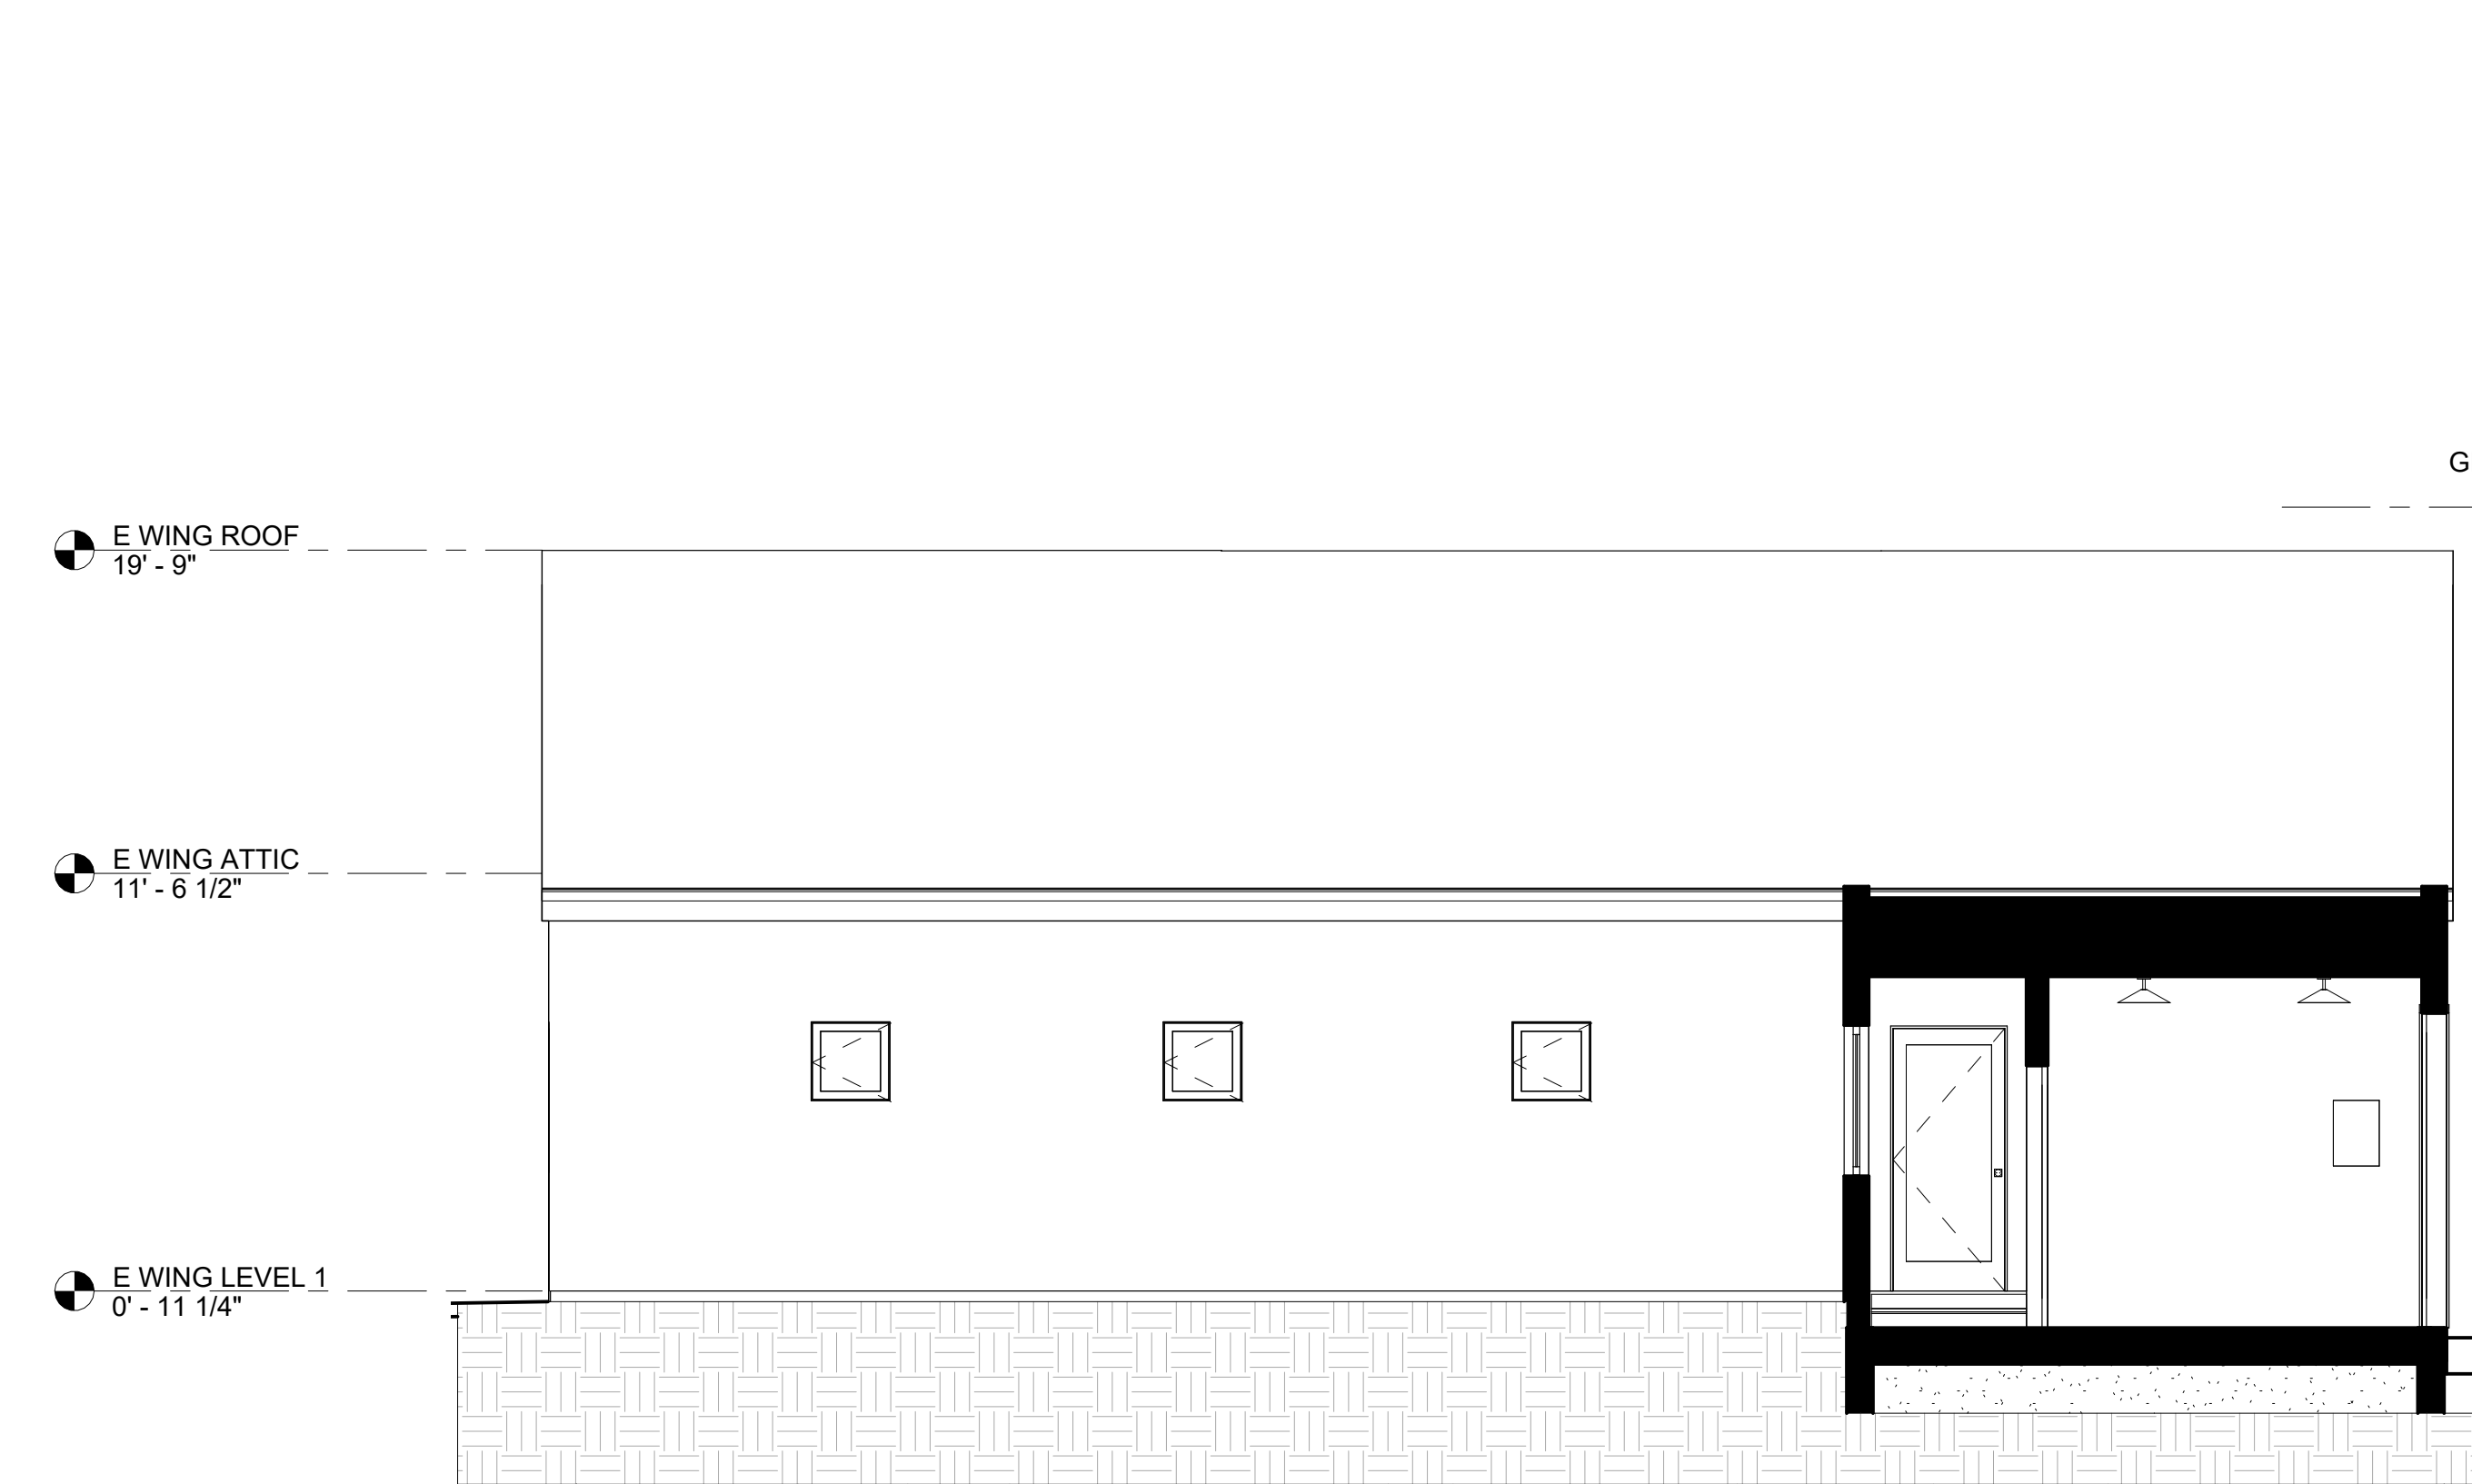

② COURTYARD WEST
1/4" = 1'-0"

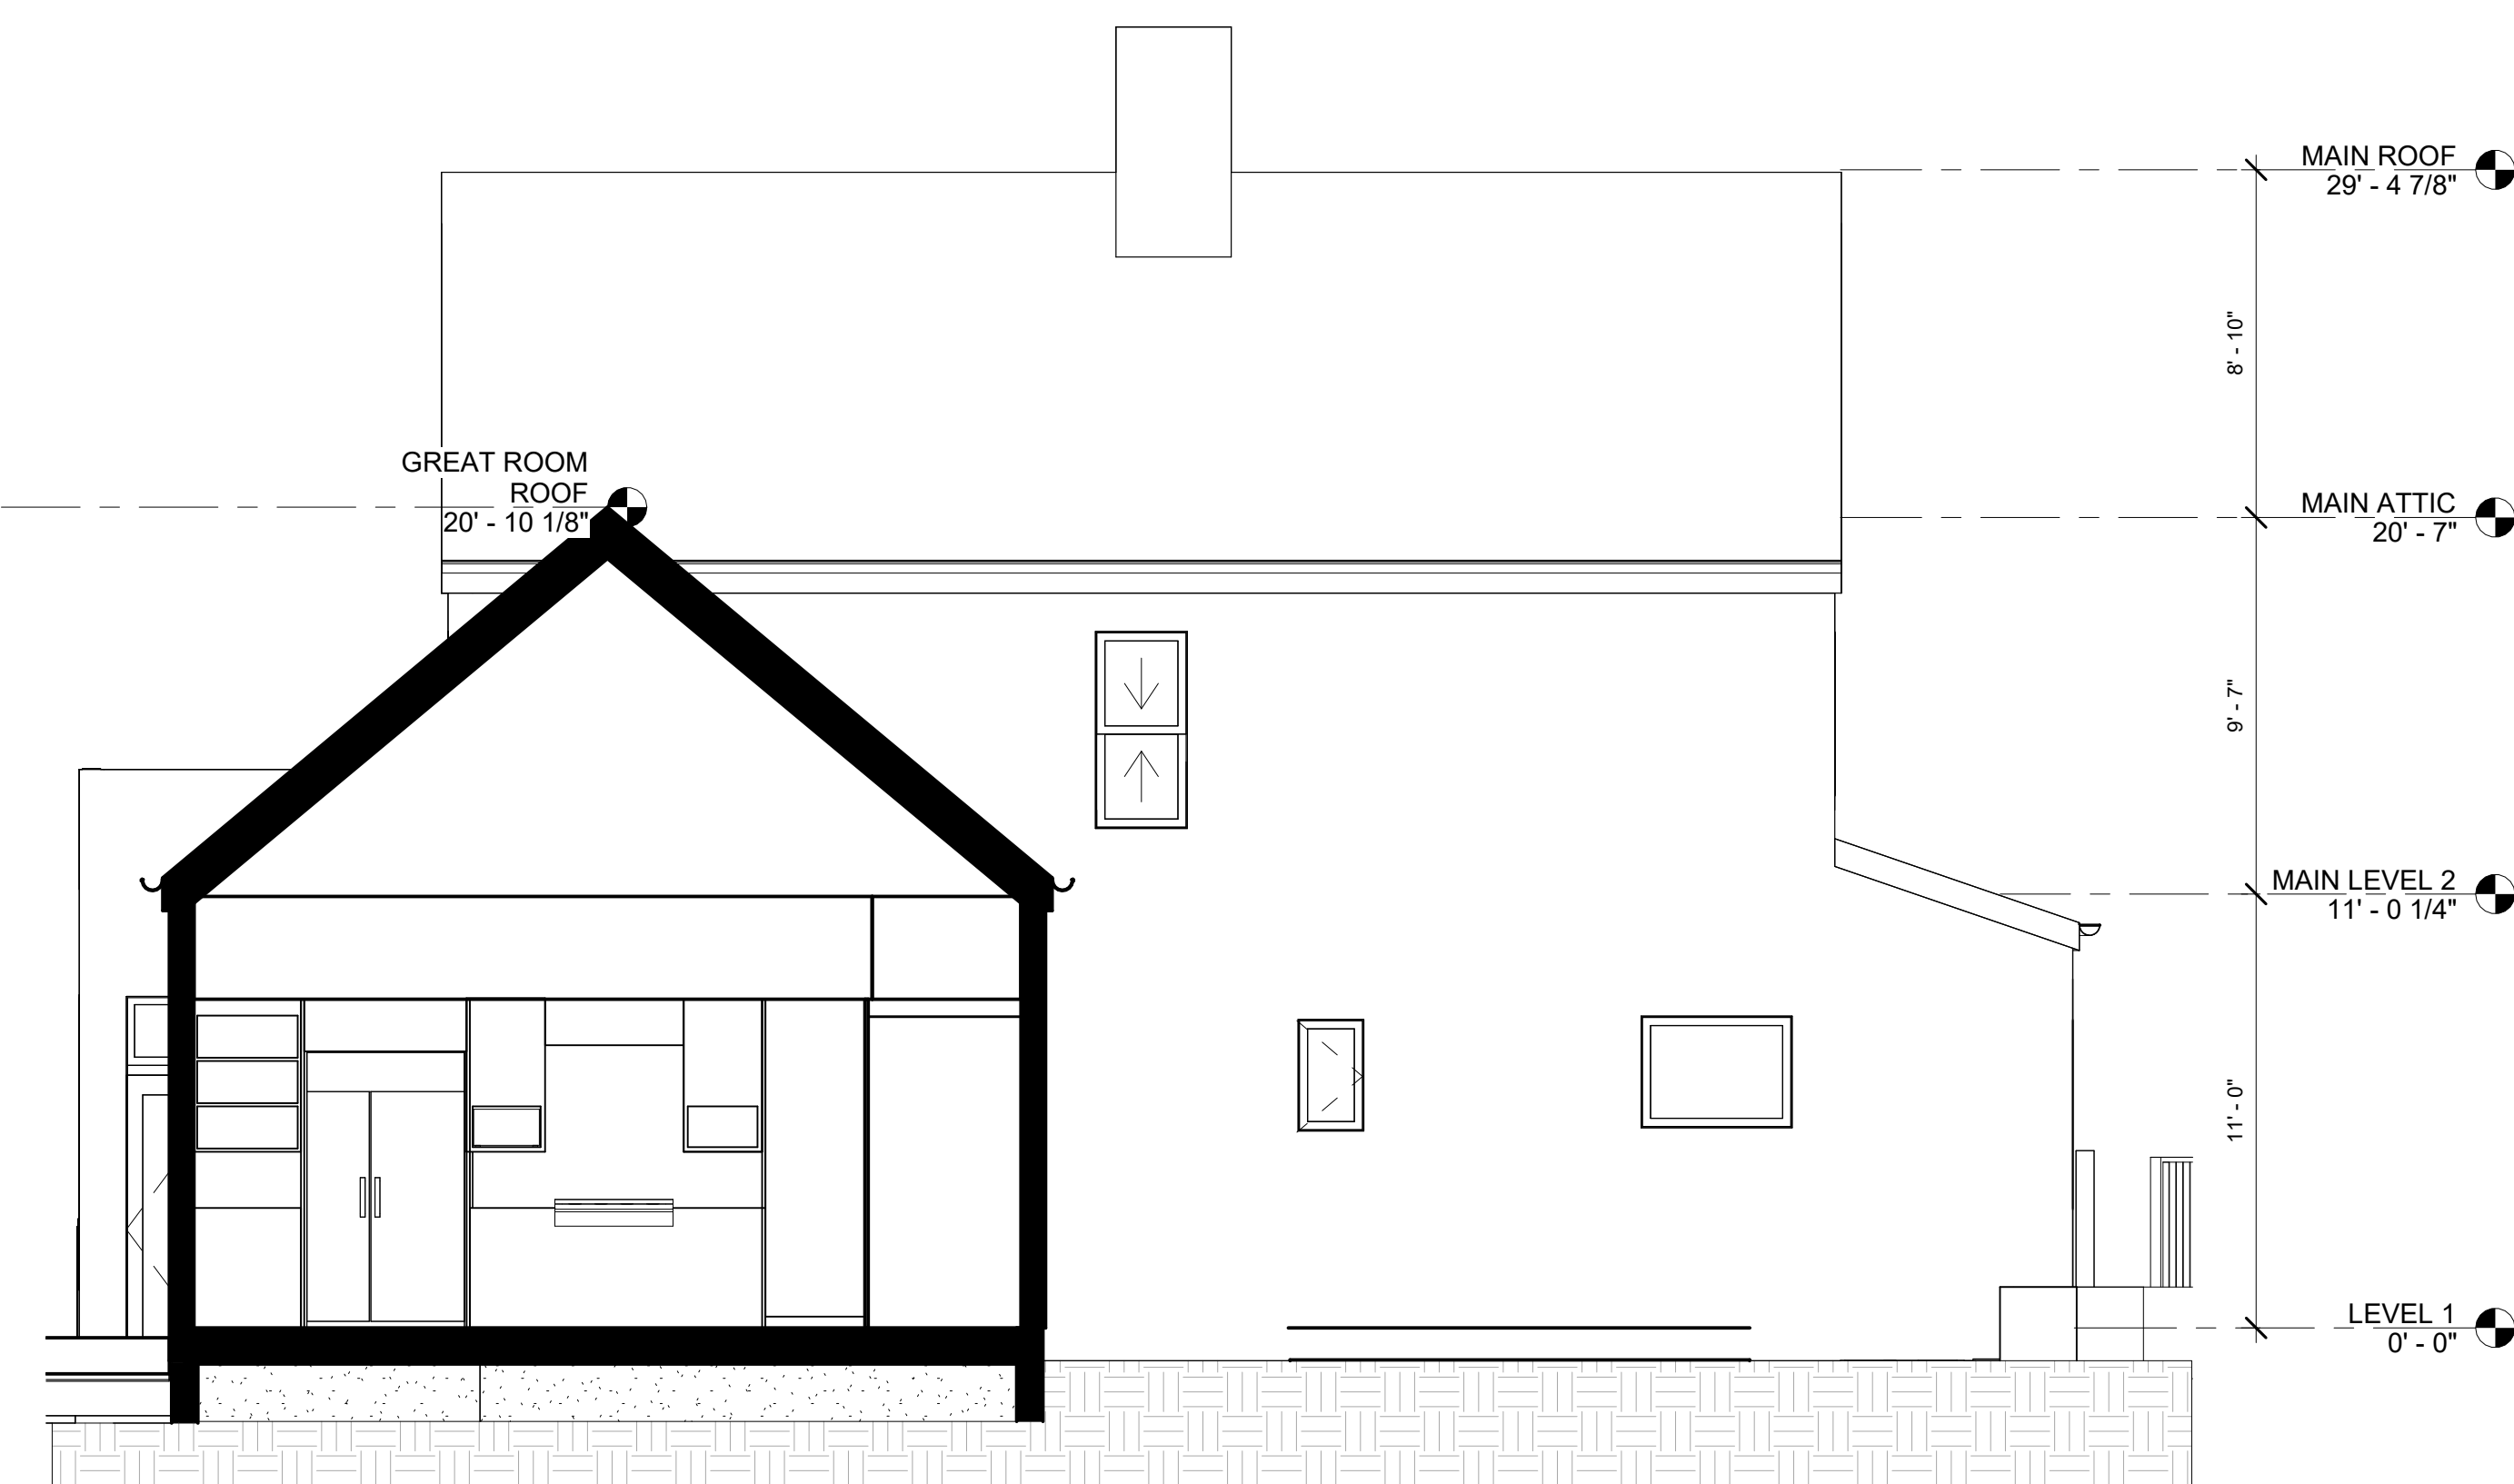

③ COURTYARD EAST
1/4" = 1'-0"



GROUND TRUTH
CAPTURE REALITY AT SCALE

Drawn Author

Existing Conditions

RESIDENT

XXX

ELEVATIONS MAIN HOUSE

SHEET NO.

A0.020


Scale 1/4" = 1'-0"



① SOUTH ELEVATION
1/4" = 1'-0"



③ WEST ELEVATION
1/4" = 1'-0"

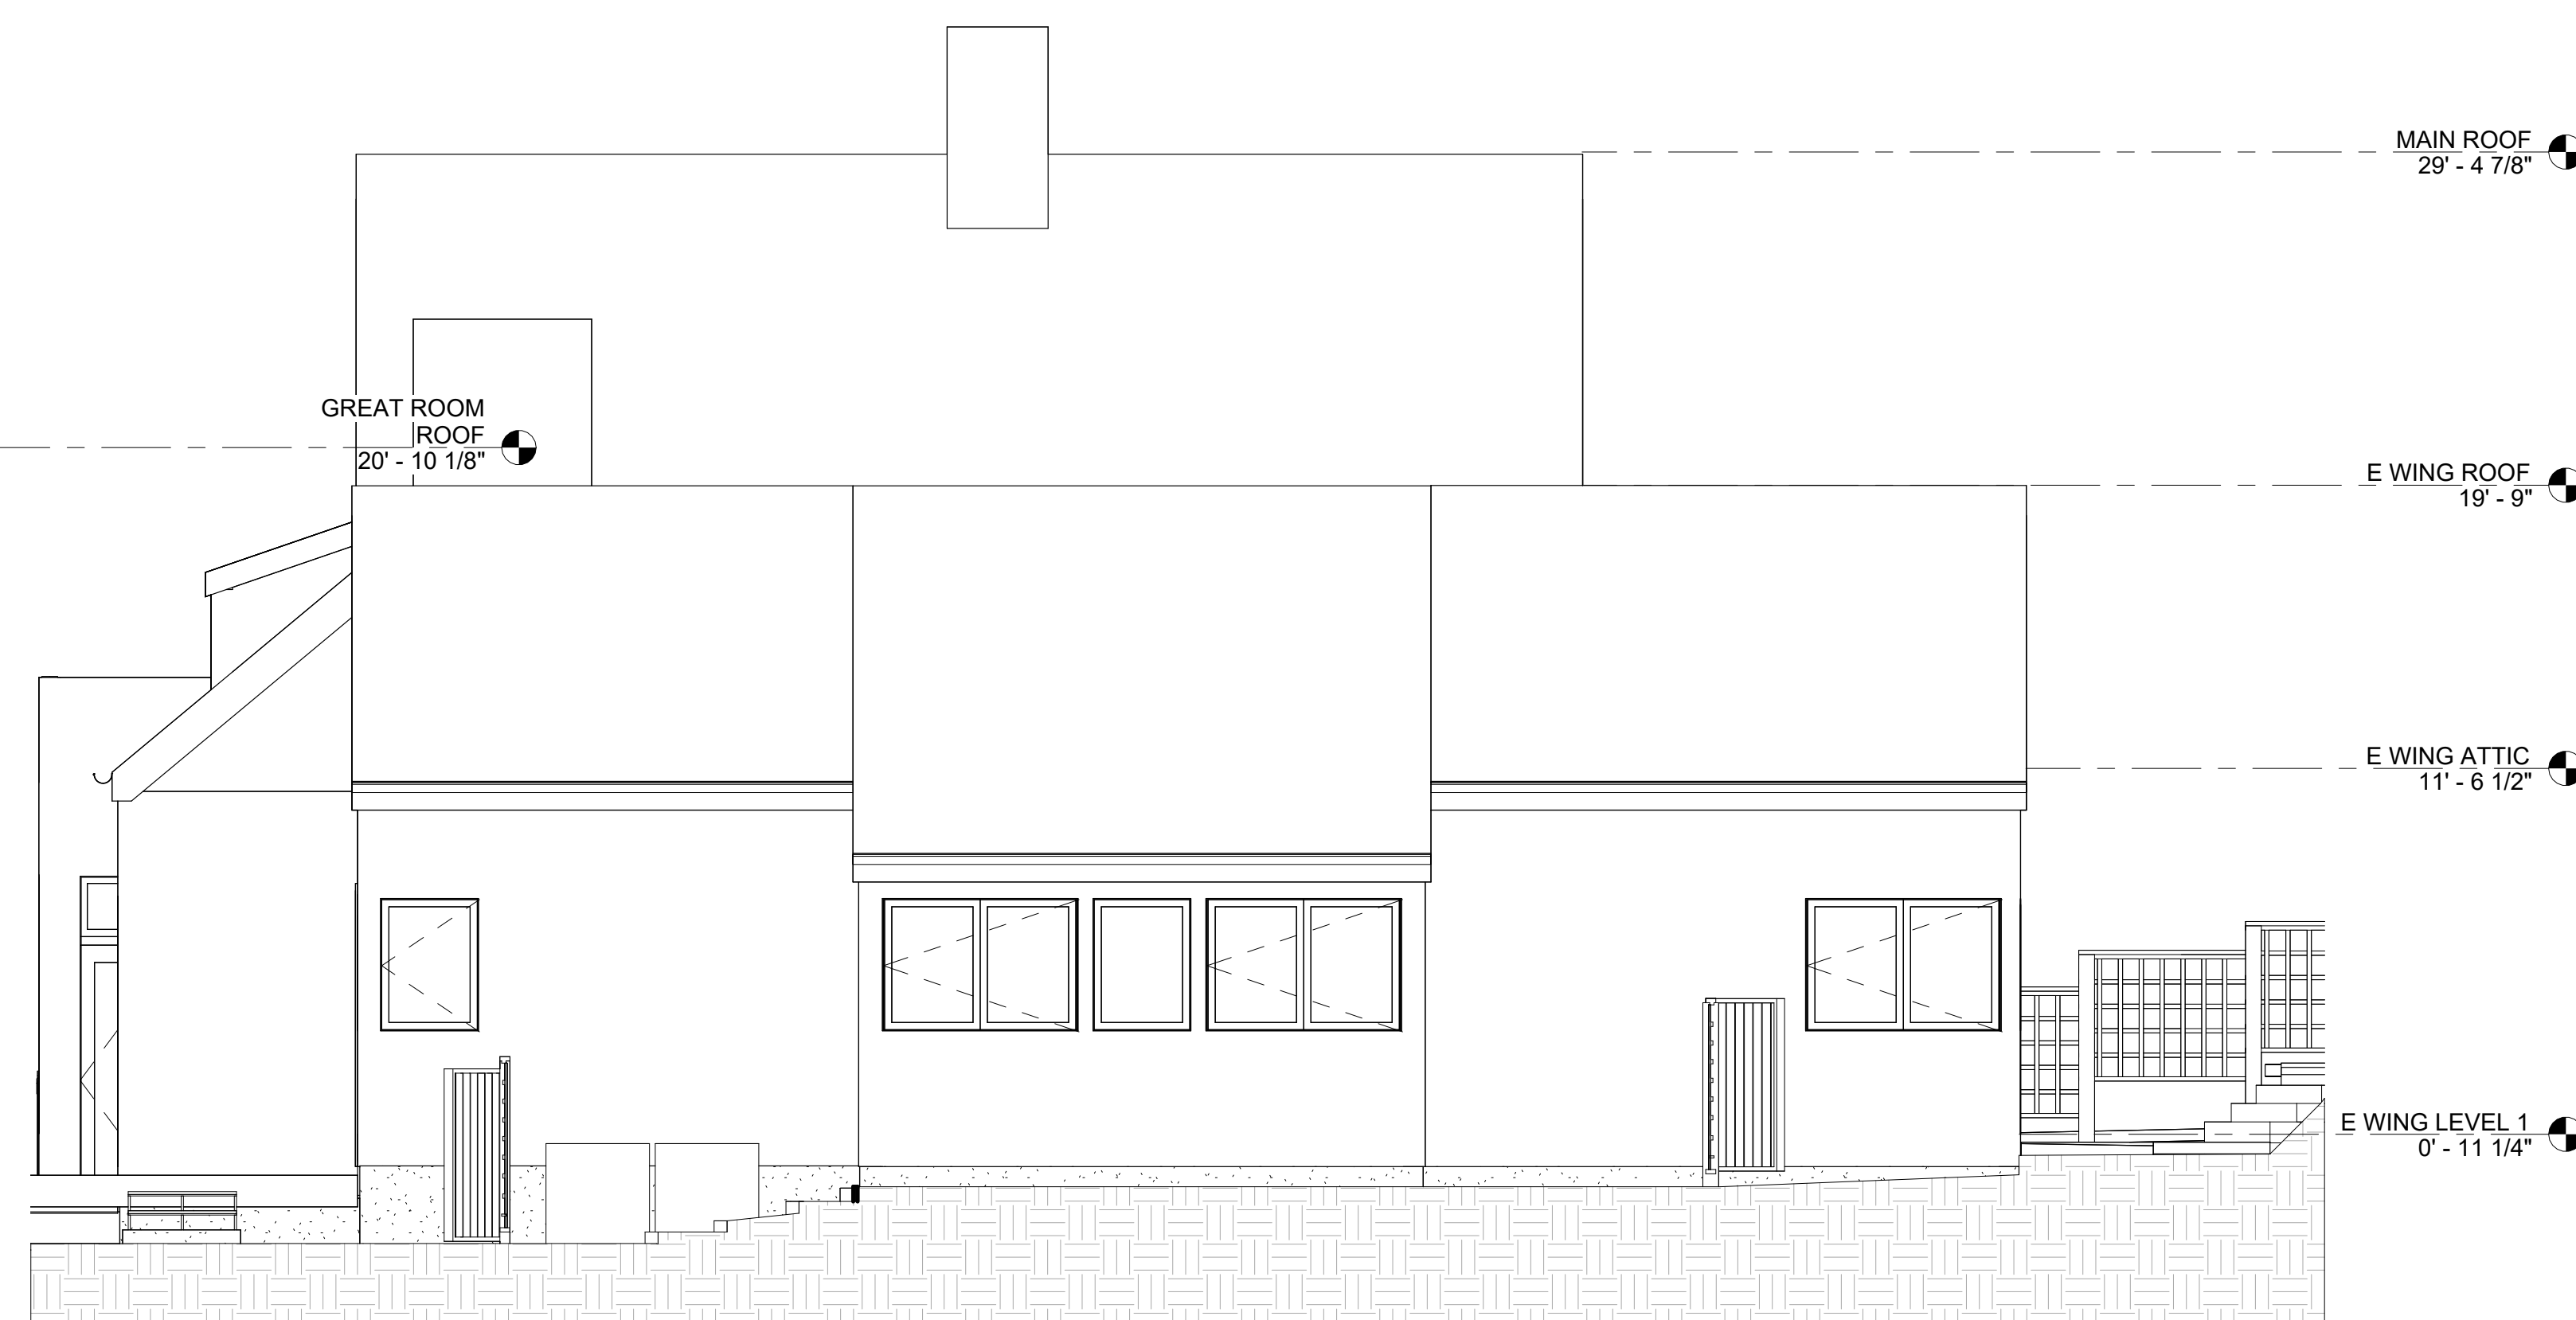

② EAST ELEVATION
1/4" = 1'-0"



GROUND TRUTH
CAPTURE REALITY AT SCALE

Author

Drawn

Existing Conditions

RESIDENT


XXX

ELEVATIONS MAIN HOUSE


SHEET NO.

A0.021


Scale 1/4" = 1'-0"

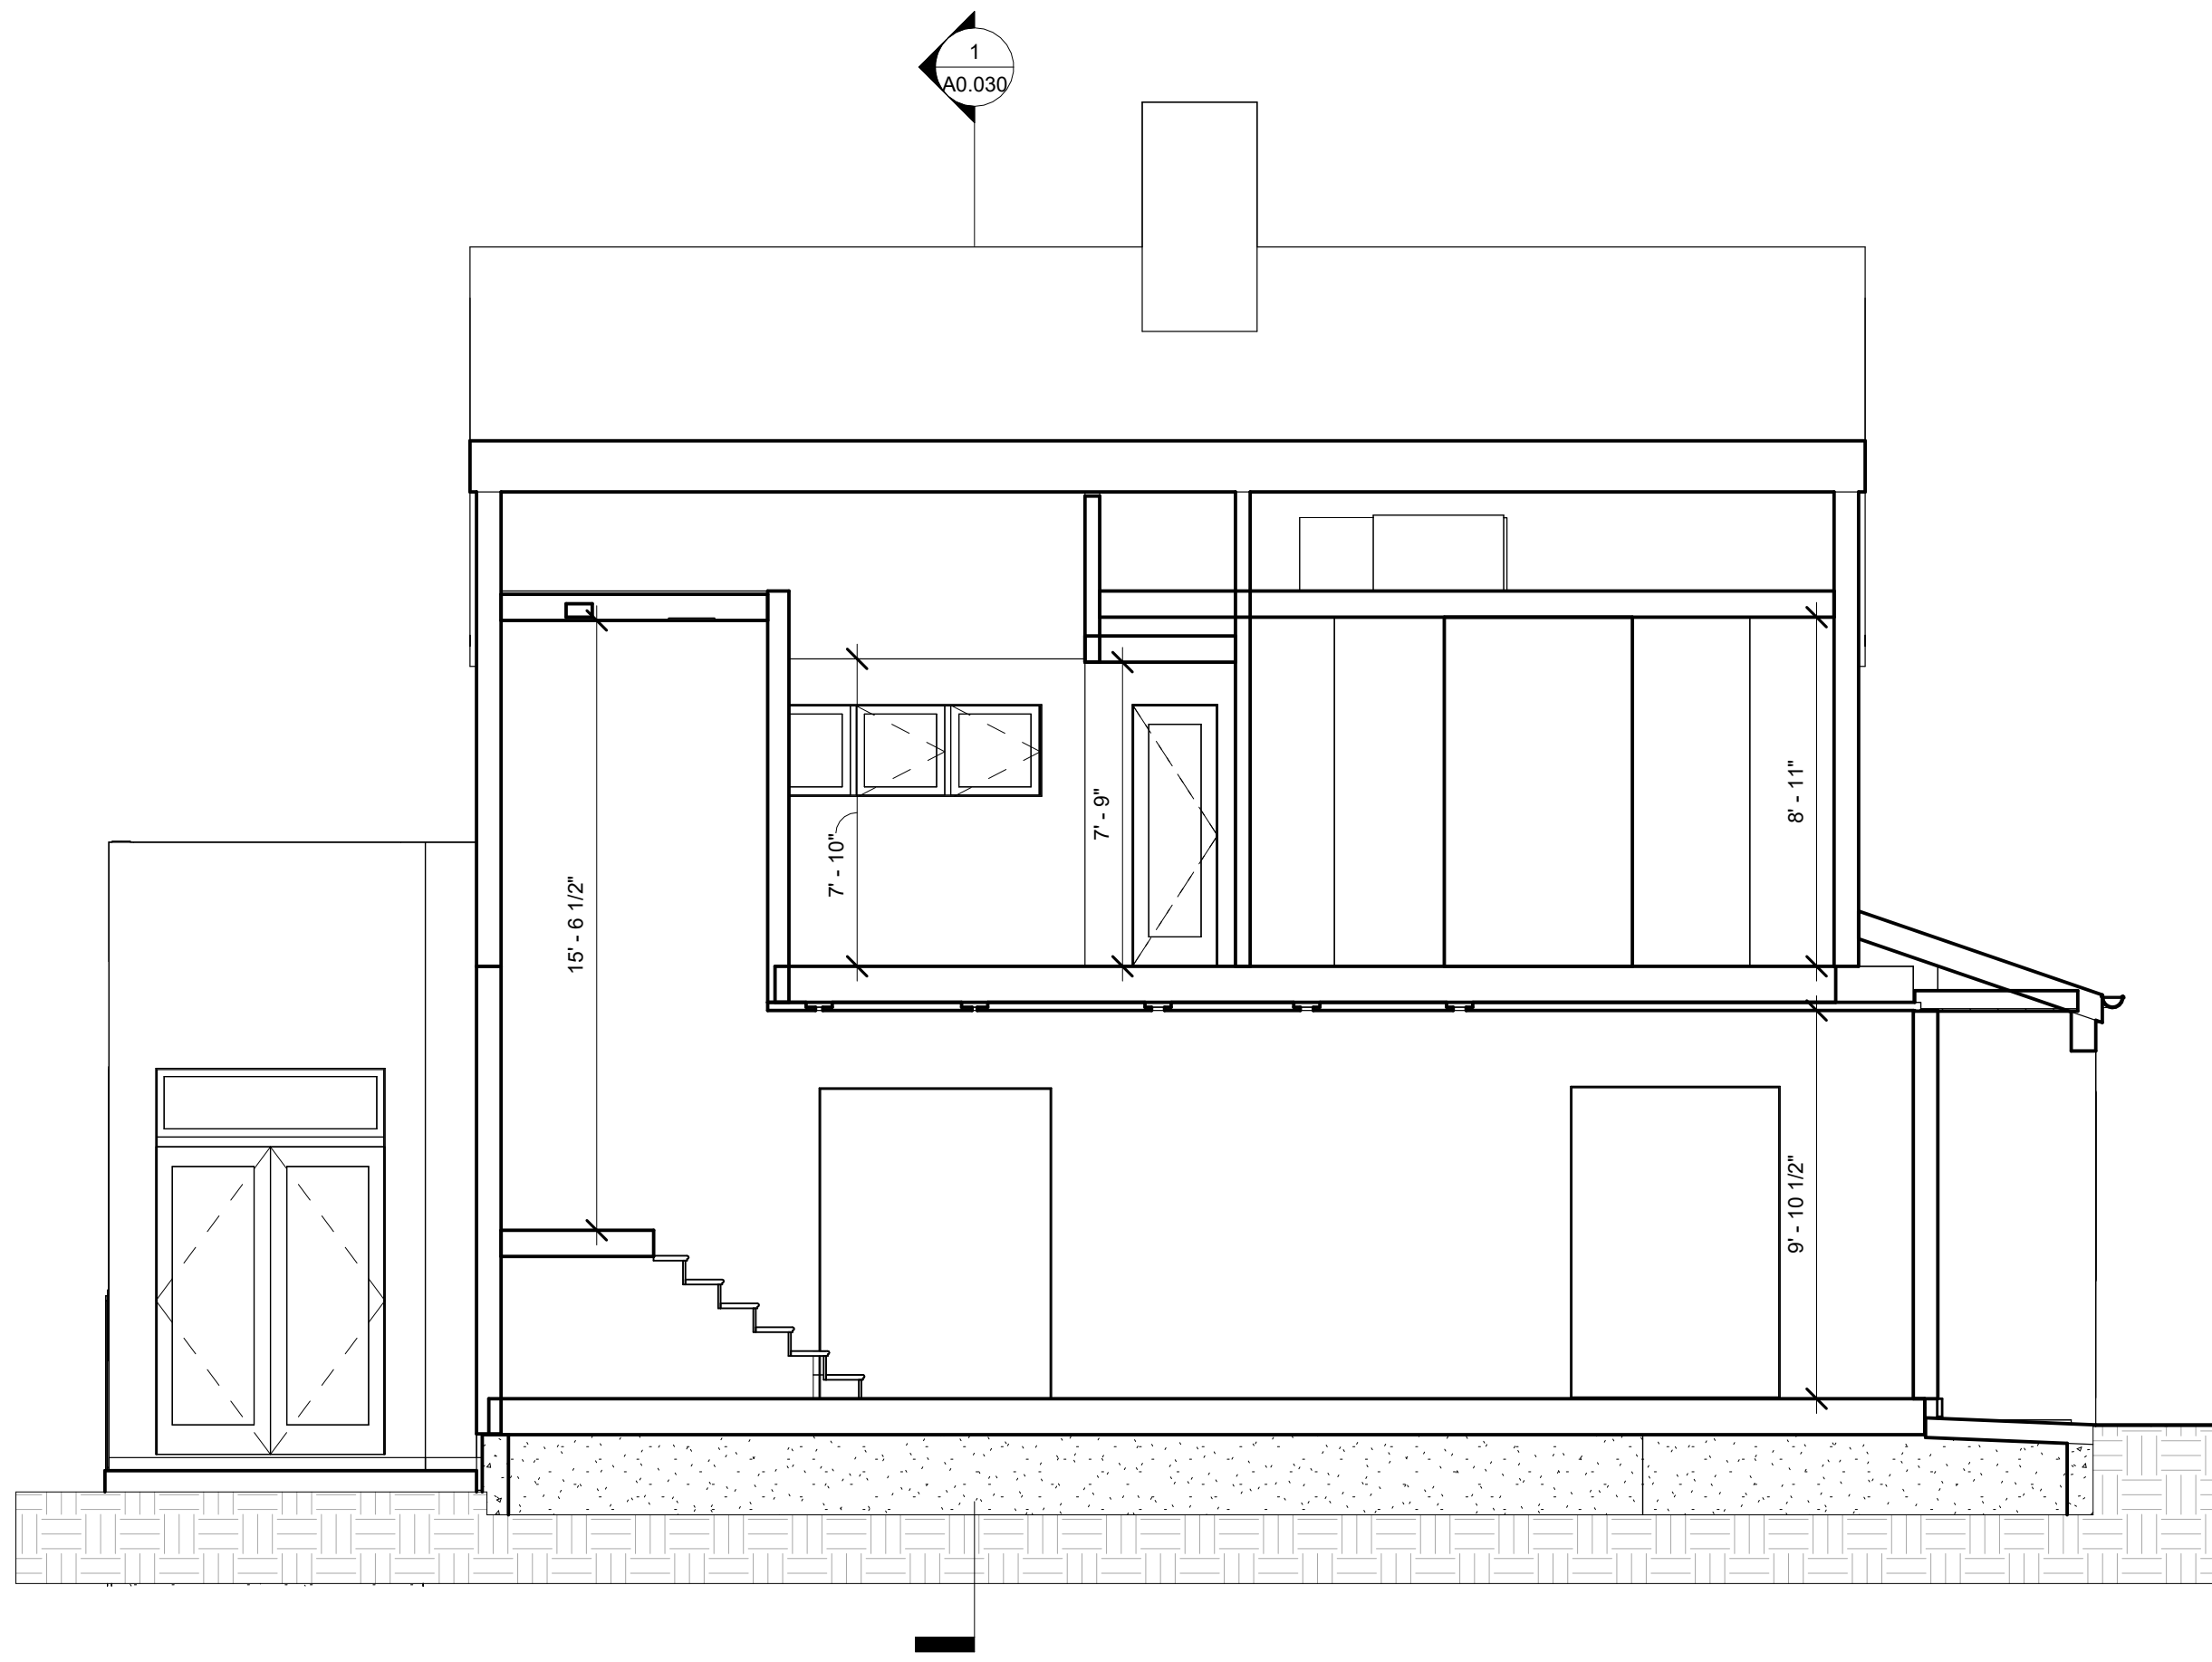

② MAIN - CROSS AT EAST WING
1/4" = 1'-0"

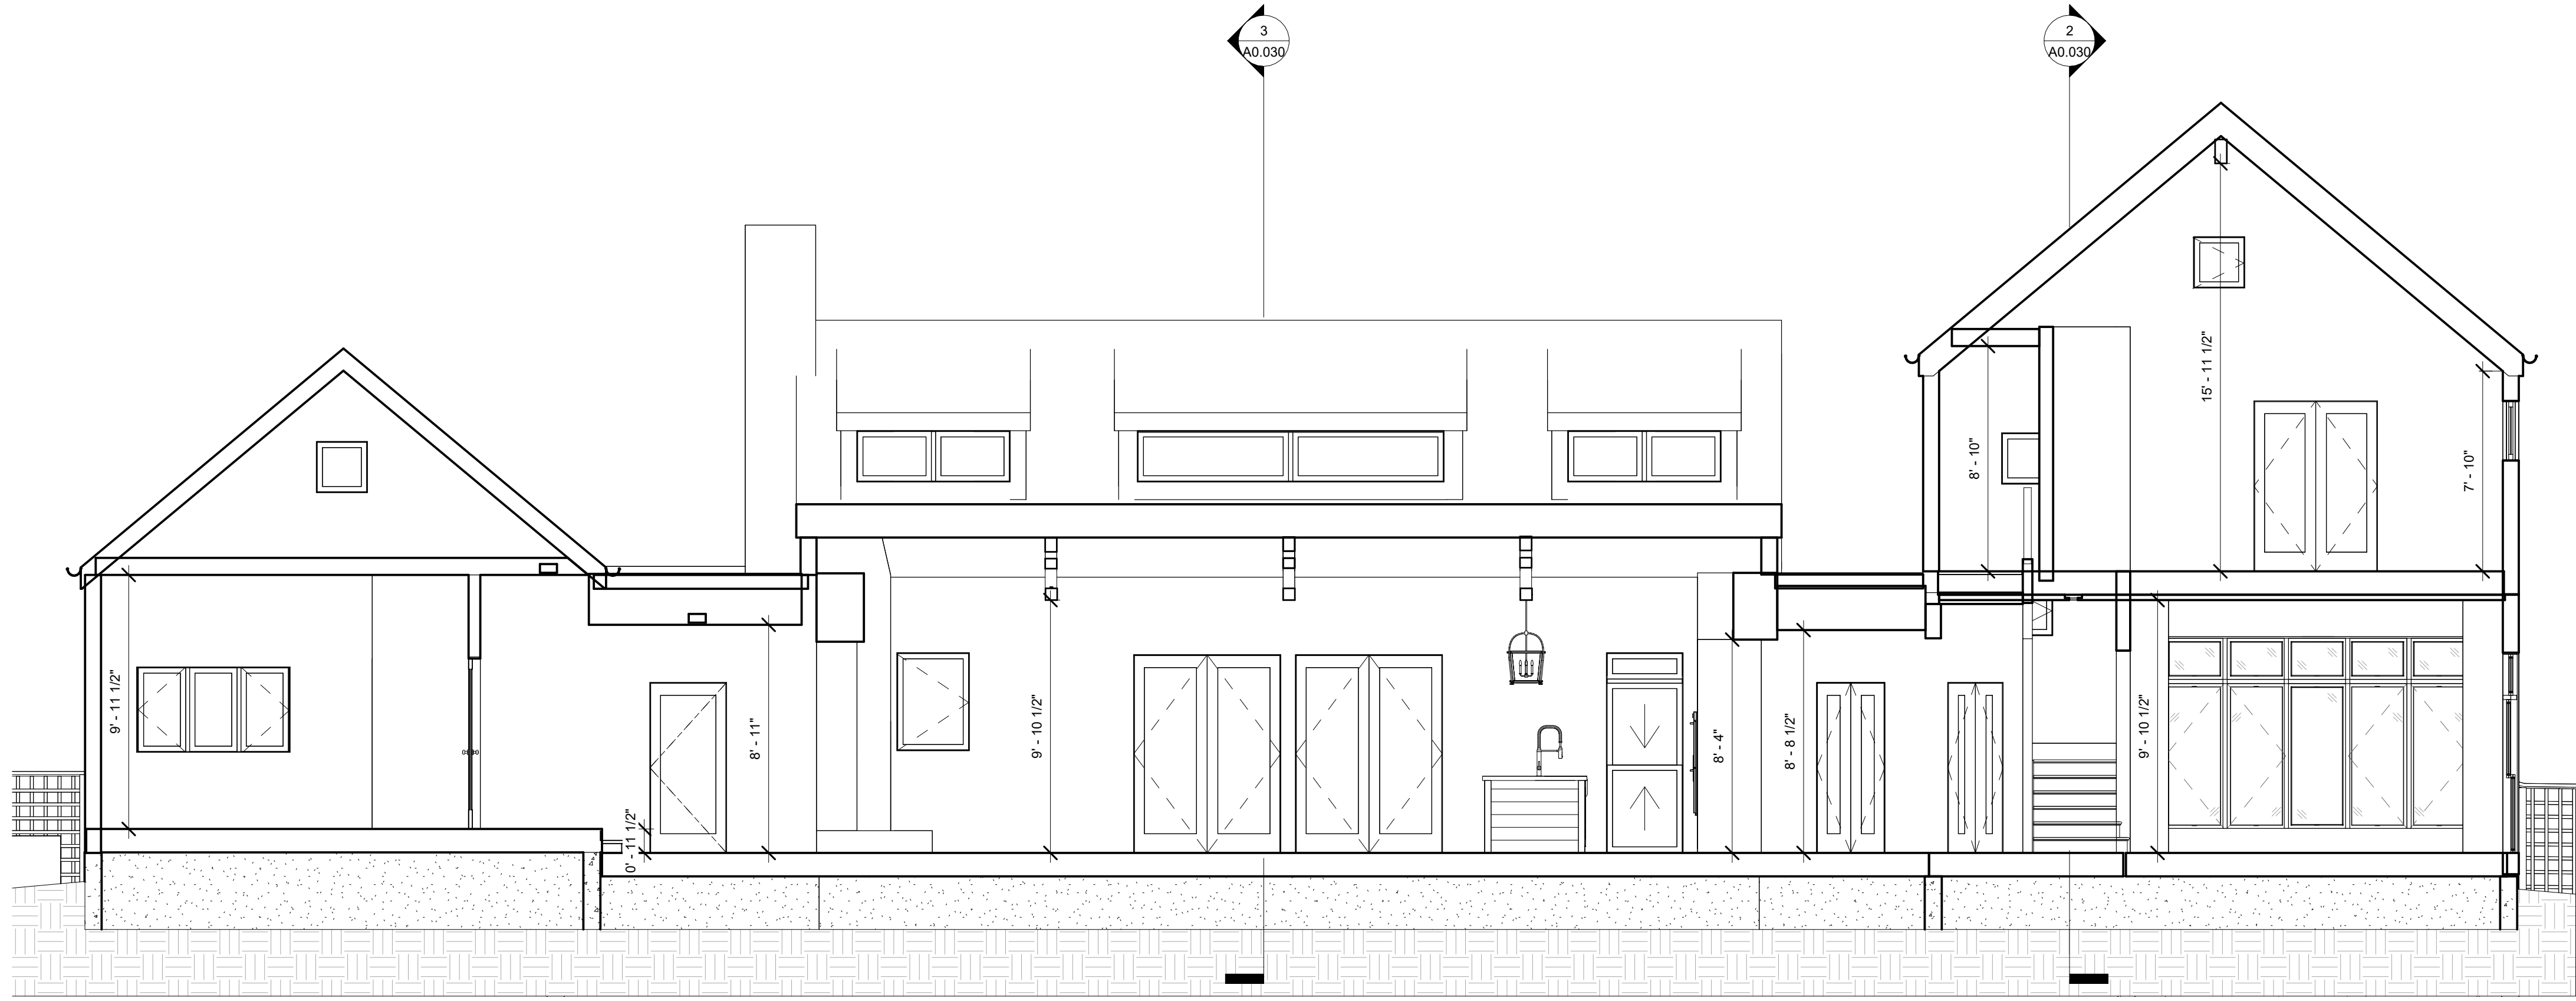

① LONG SECTION - SOUTH
1/4" = 1'-0"

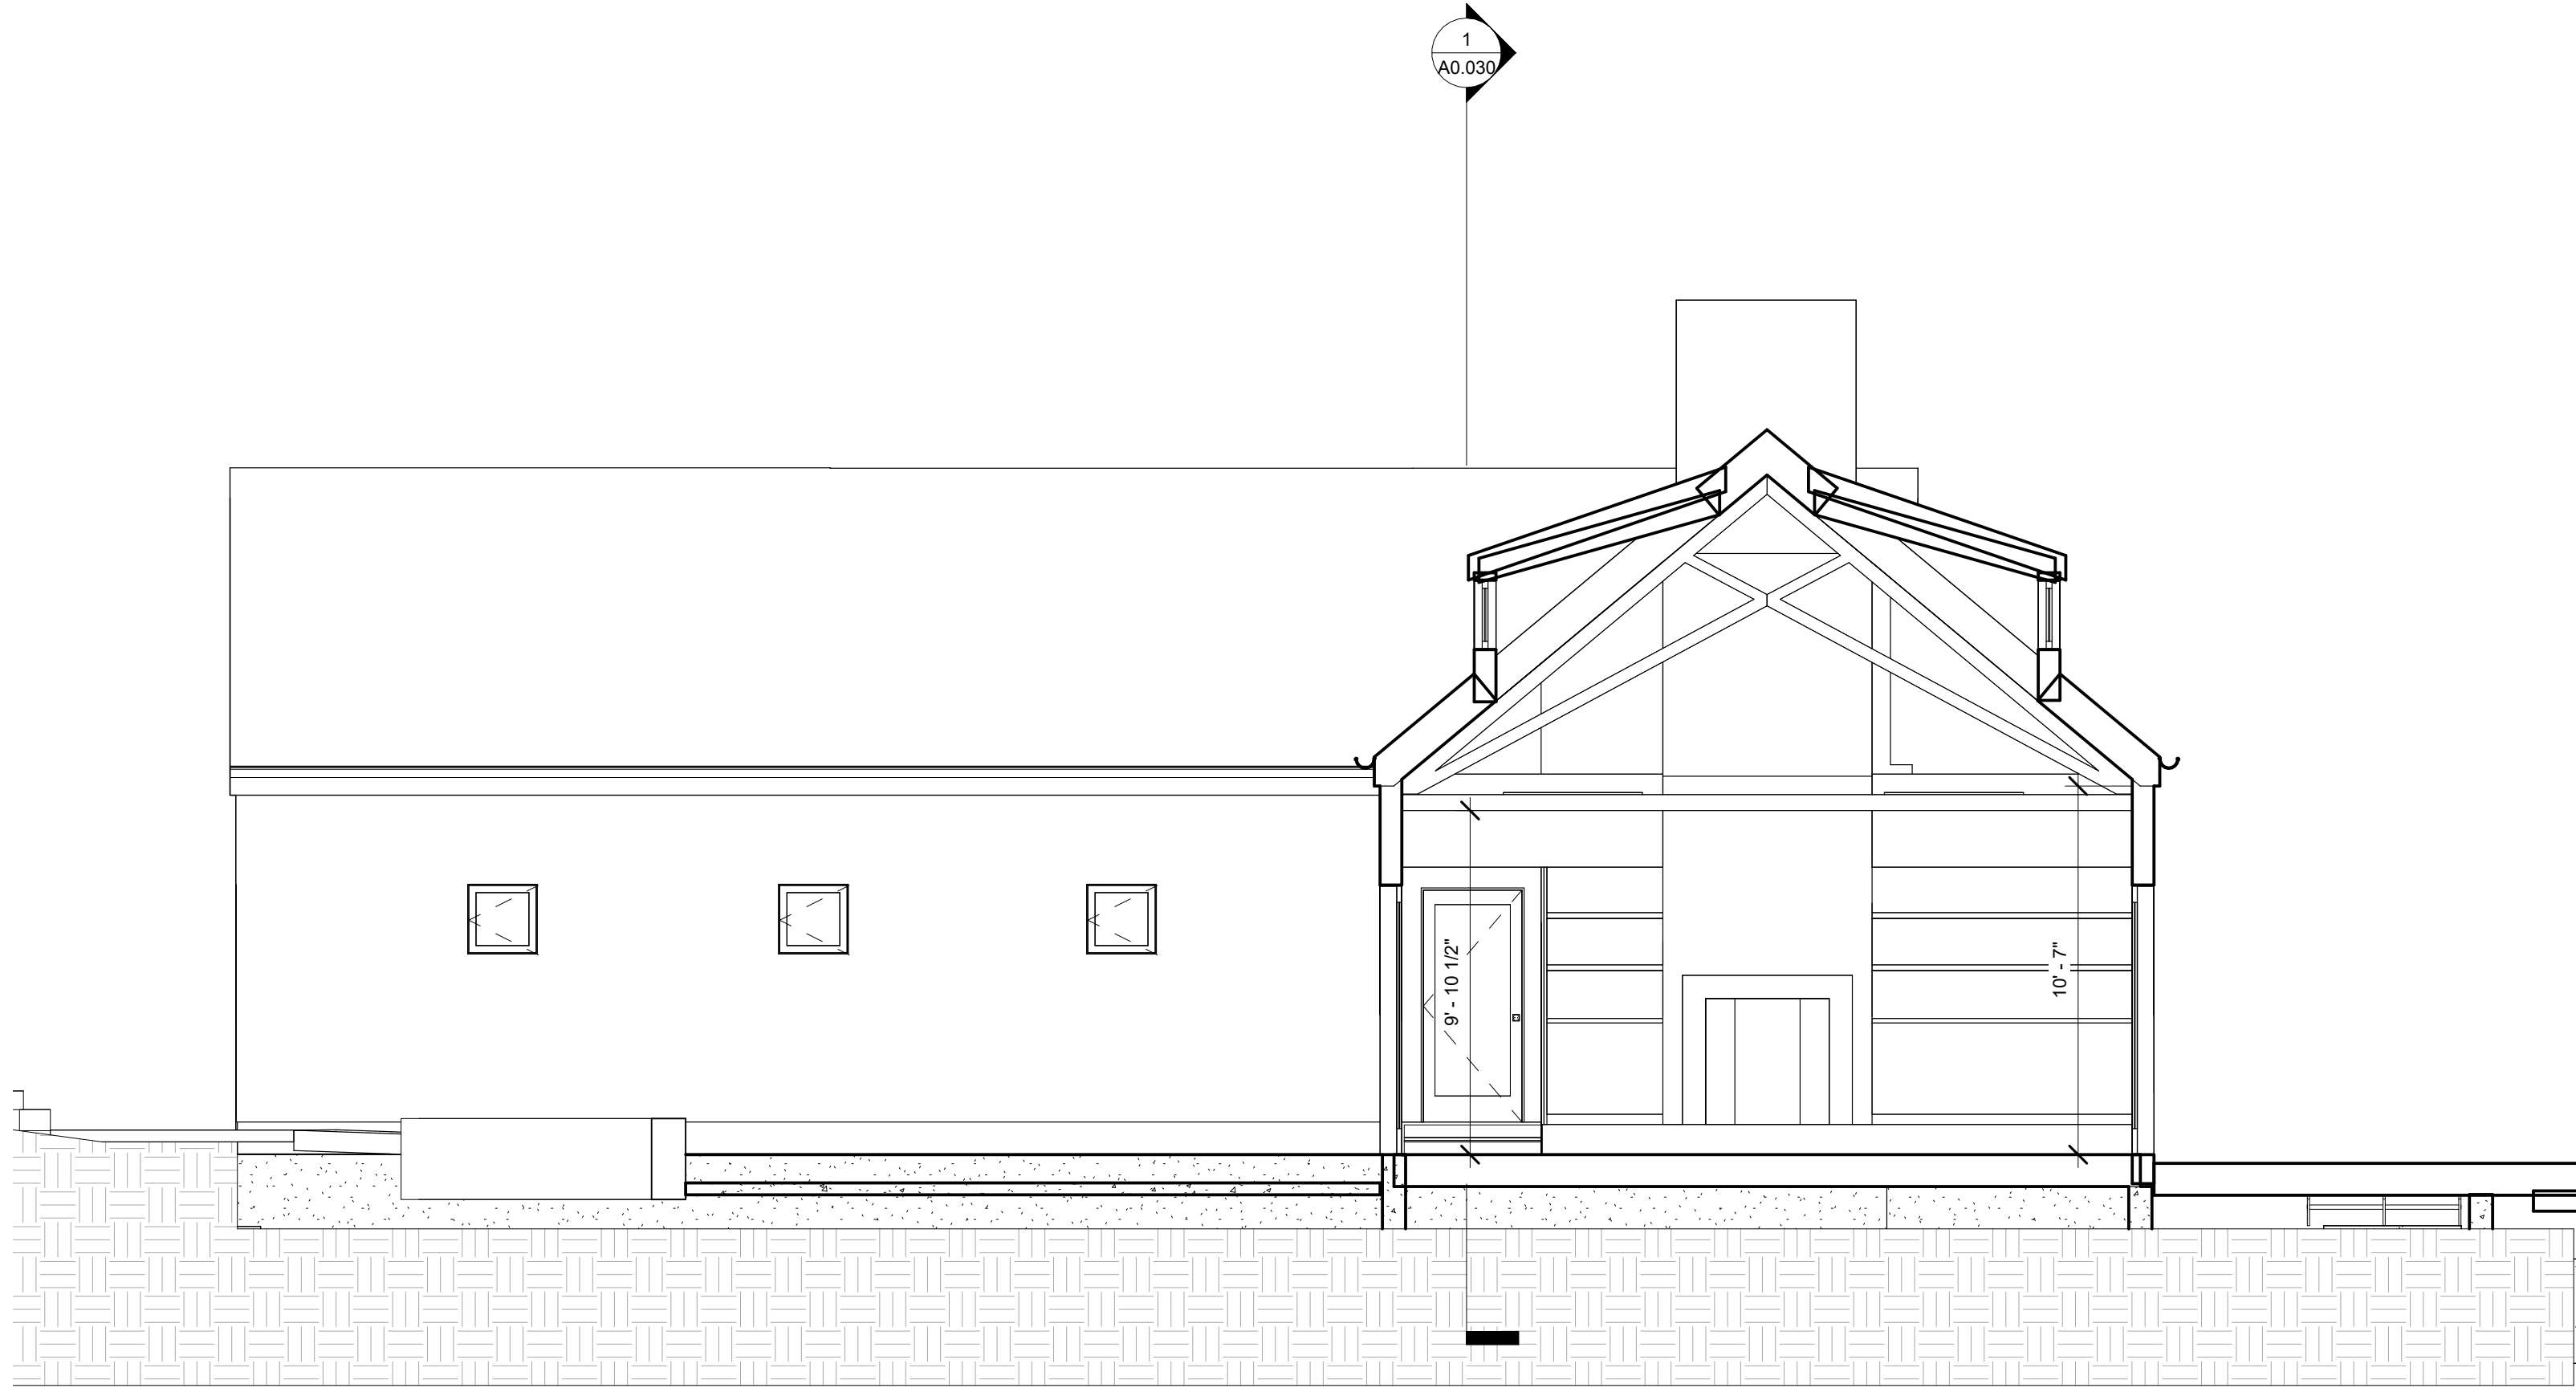

③ MAIN - CROSS AT KITCHEN
1/4" = 1'-0"

XXX

SHEET NO.

A0.030

Scale 1/4" = 1'-0"

Existing Conditions

SECTIONS MAIN HOUSE


RESIDENT

Drawn


Author




GROUND TRUTH
CAPTURE REALITY AT SCALE

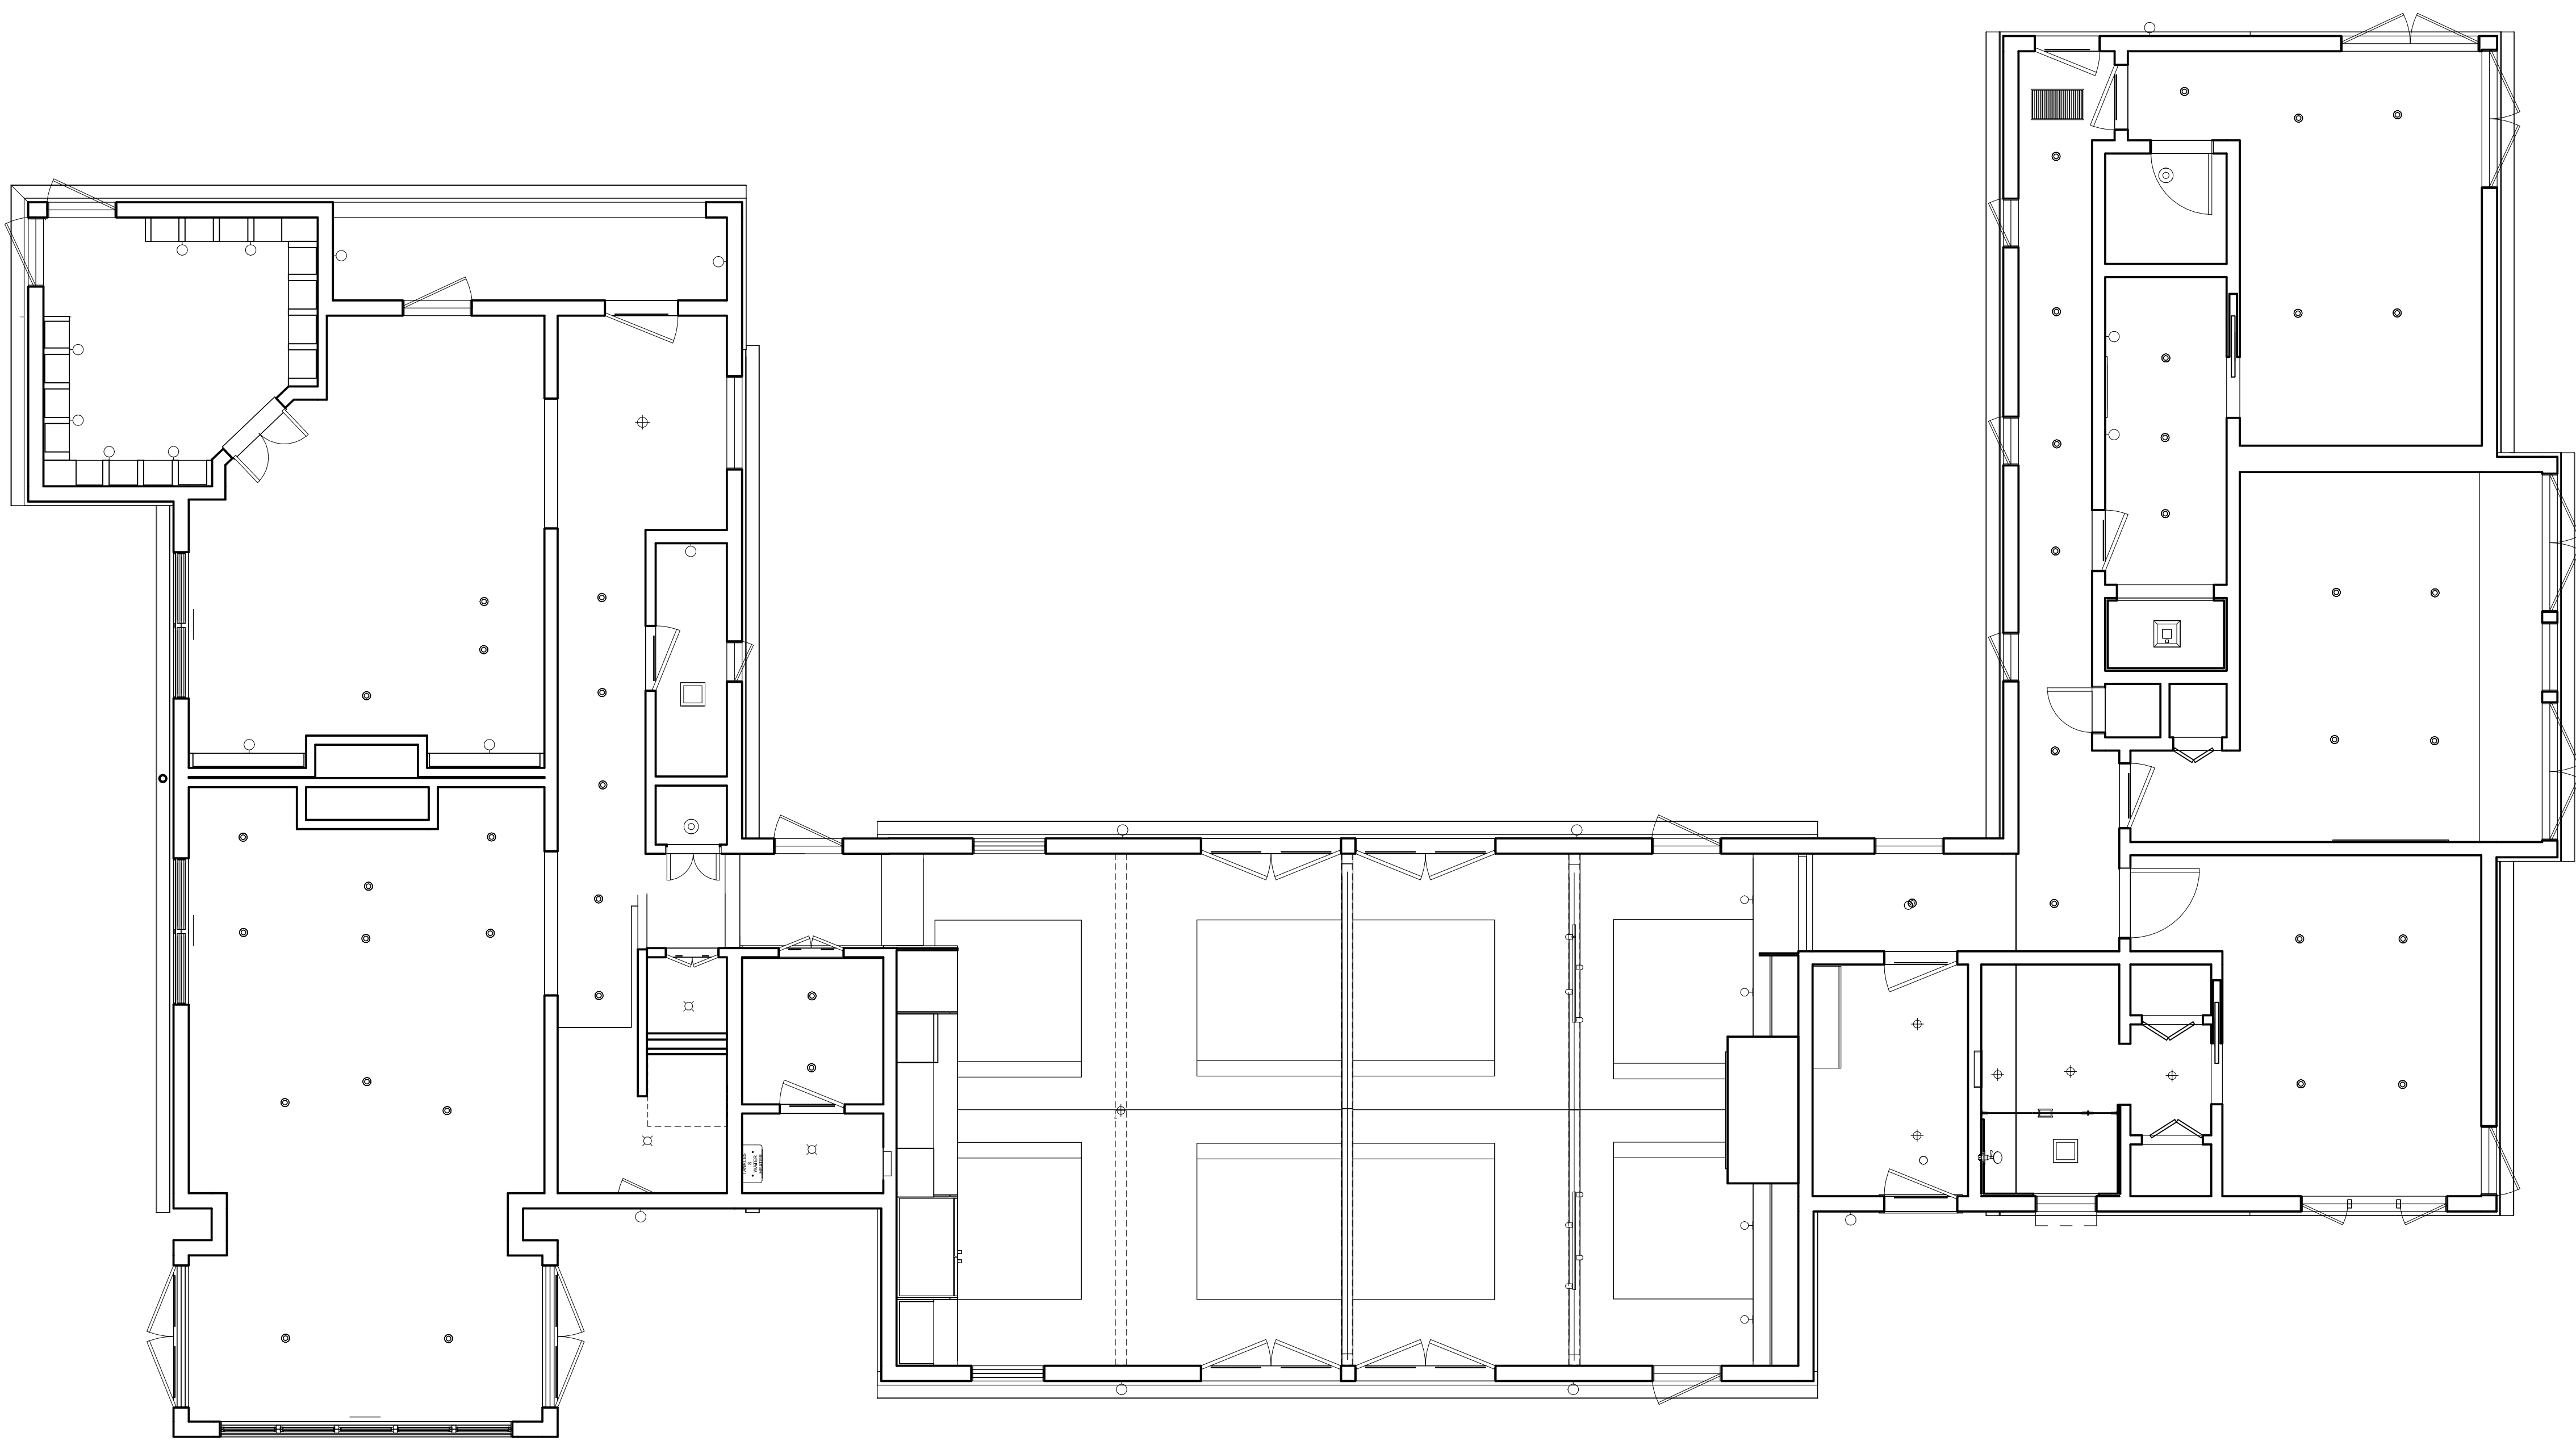

① LEVEL 1
1/4" = 1'-0"

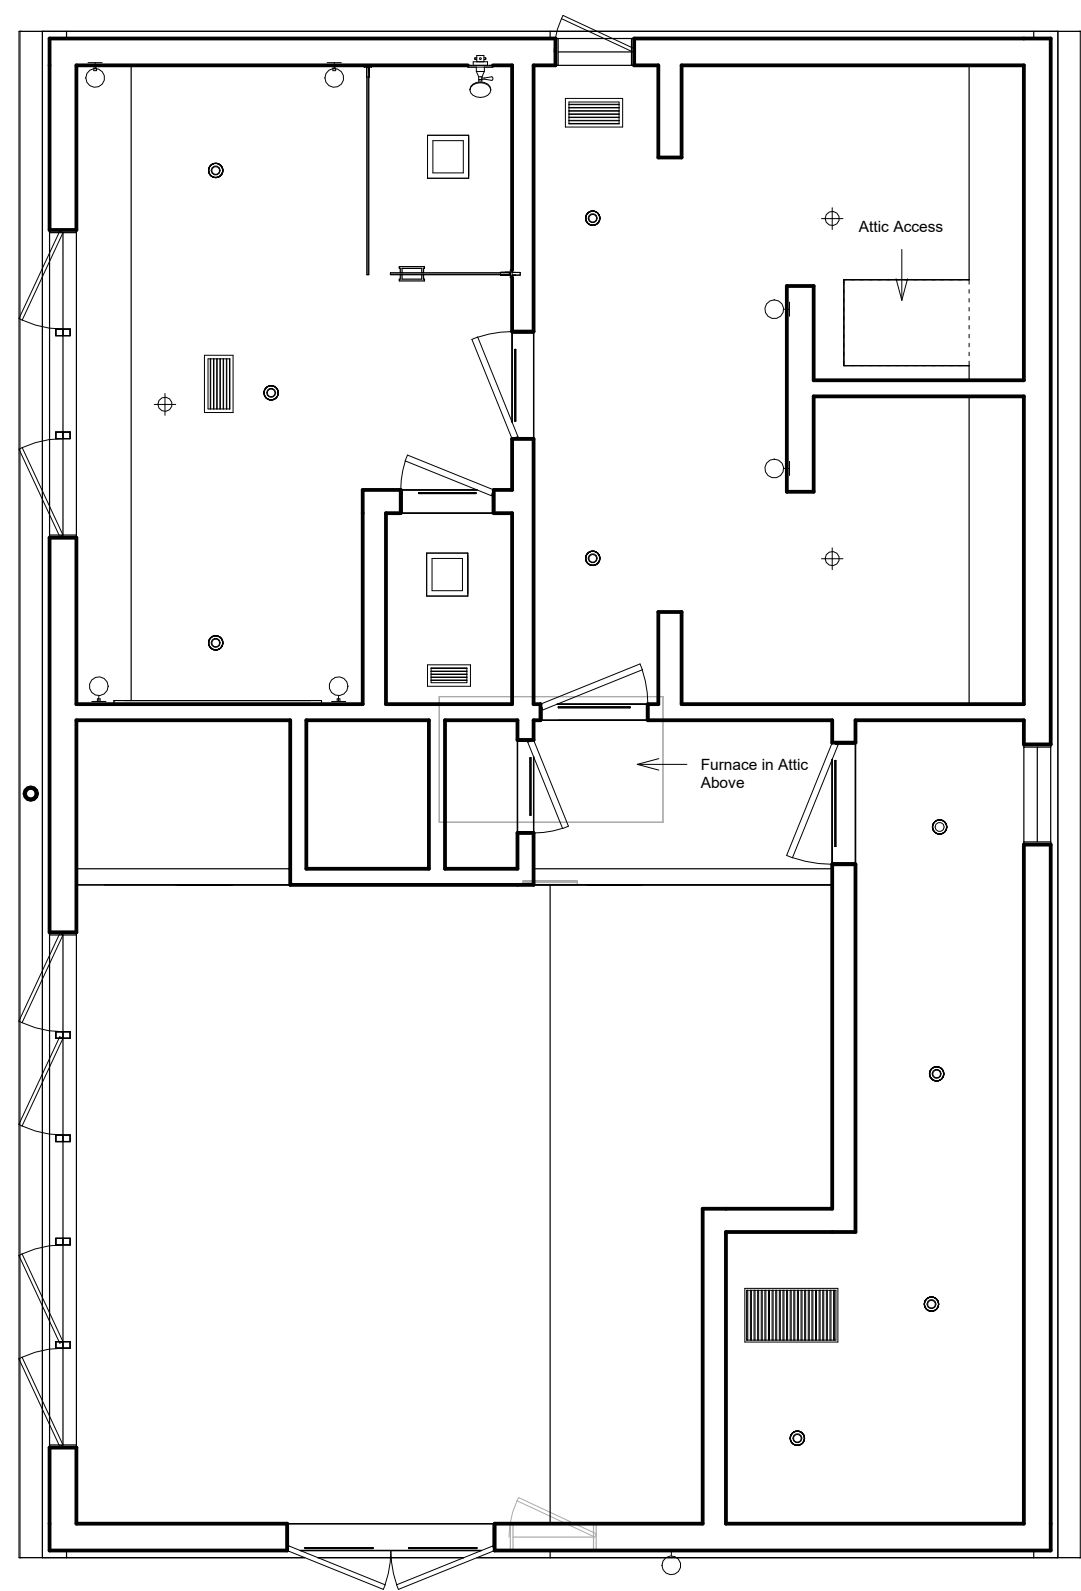

② MAIN LEVEL 2
1/4" = 1'-0"

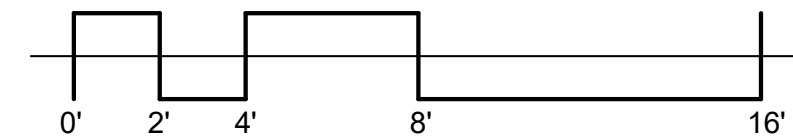

XXX

RCP EXISTING CONDITIONS

Existing Conditions

RESIDENT

Author




GROUND TRUTH
CAPTURE REALITY AT SCALE


SHEET NO.

A0.040


Scale 1/4" = 1'-0"

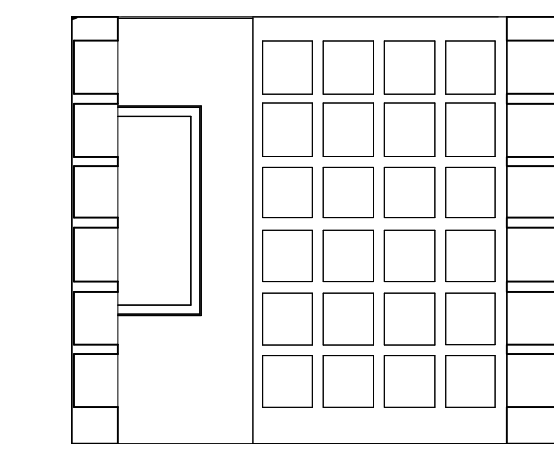


1 OFFICE - NORTH
1/4" = 1'-0"

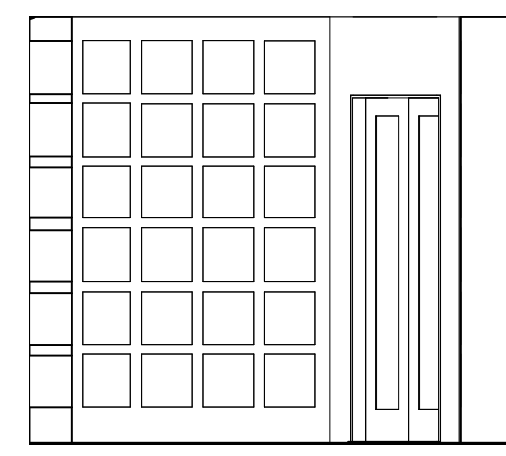


2 OFFICE - EAST
1/4" = 1'-0"

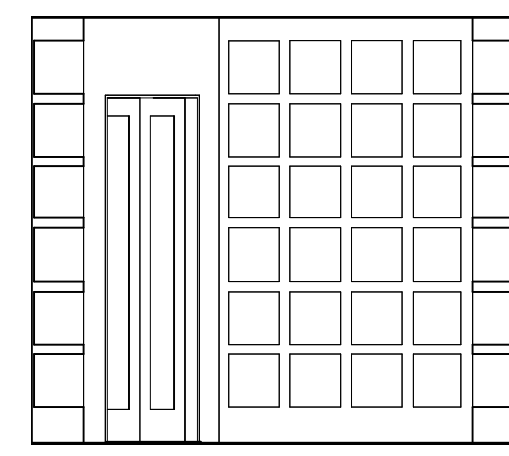


3 OFFICE - SOUTH
1/4" = 1'-0"

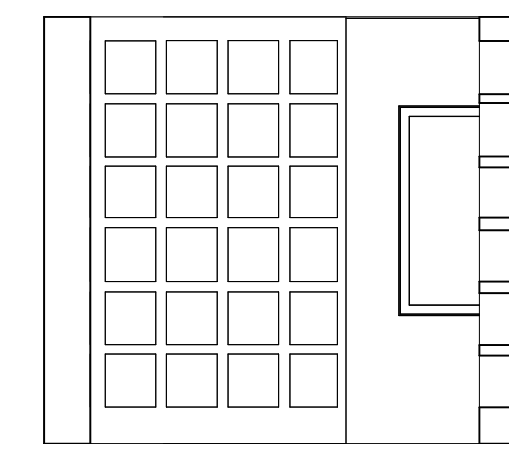


4 OFFICE - WEST
1/4" = 1'-0"

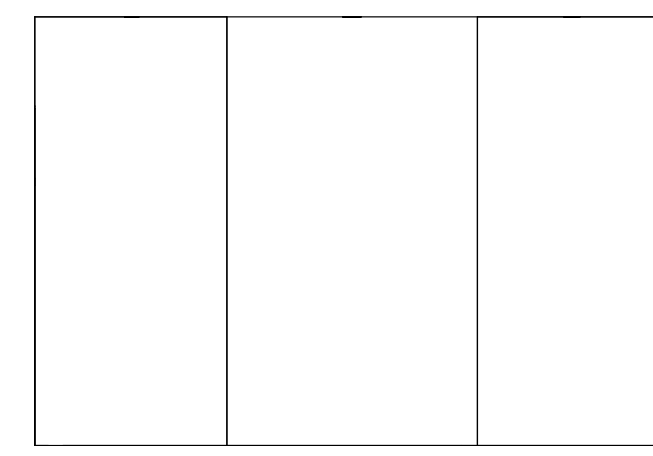


5 DINING ROOM - NORTH
1/4" = 1'-0"

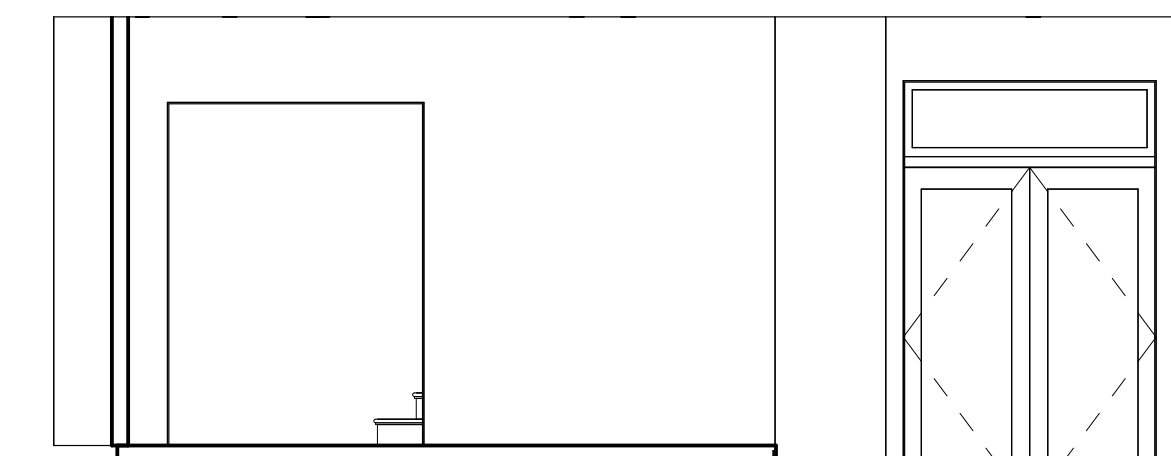


6 DINING ROOM - EAST
1/4" = 1'-0"

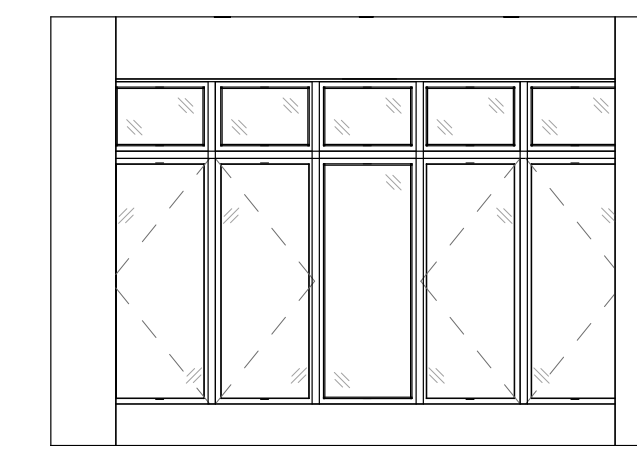


7 DINING ROOM - SOUTH
1/4" = 1'-0"

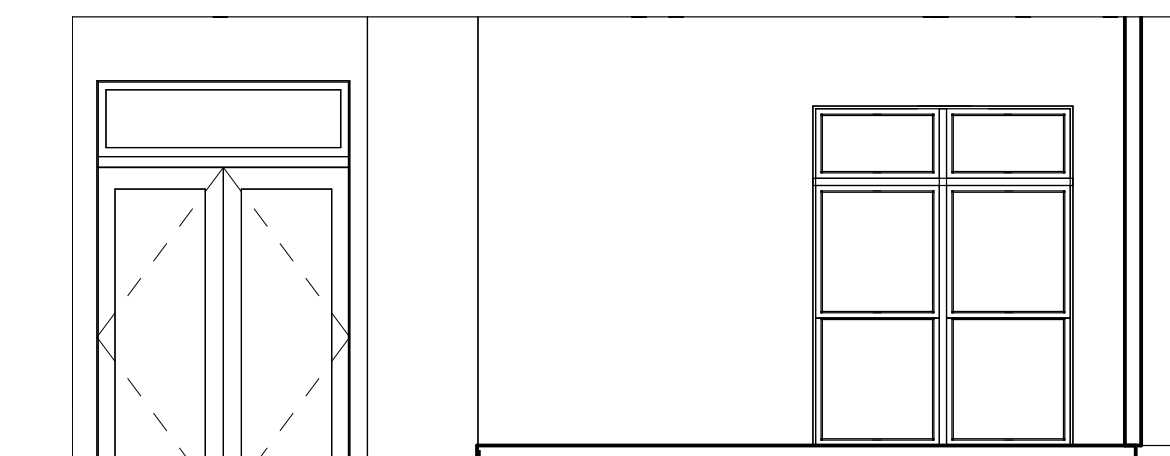


8 DINING ROOM - WEST
1/4" = 1'-0"

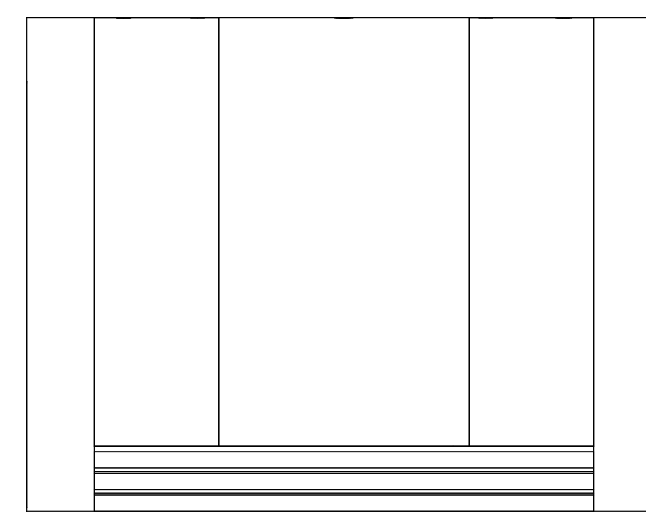

9 OFFICE 2 - NORTH
1/4" = 1'-0"

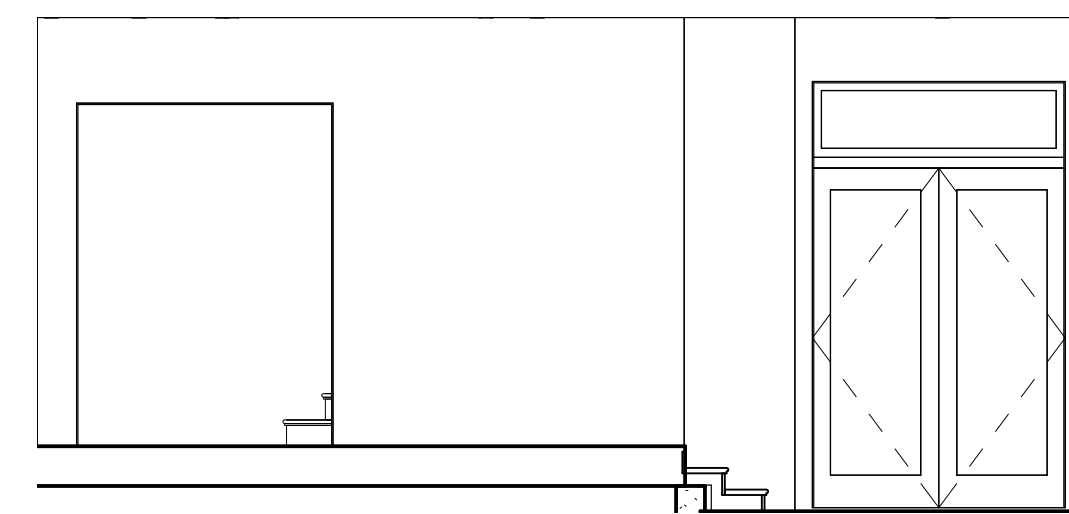


10 OFFICE 2 - EAST
1/4" = 1'-0"

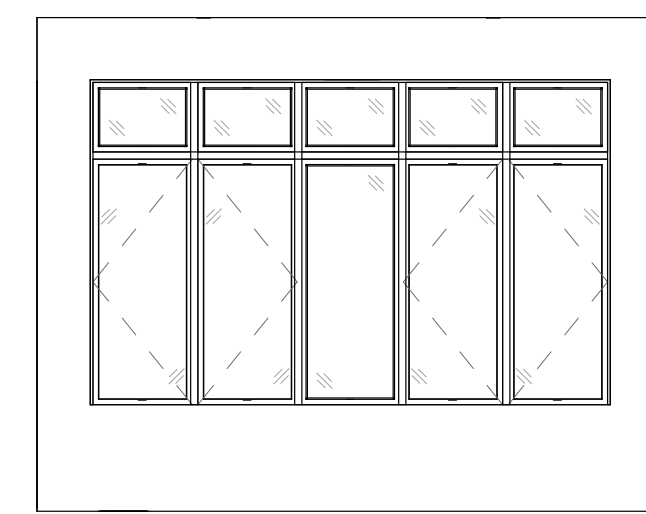


11 OFFICE 2 - SOUTH
1/4" = 1'-0"



12 OFFICE 2 - WEST
1/4" = 1'-0"

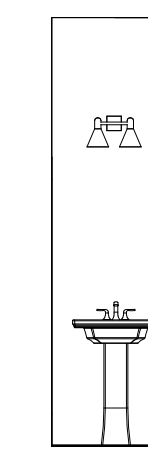


13 P.R. - N
1/4" = 1'-0"

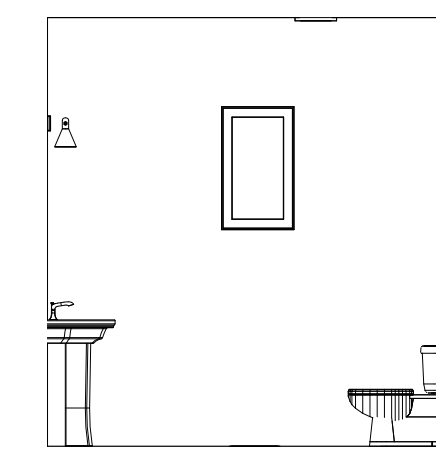


14 P.R. - EAST
1/4" = 1'-0"




15 P.R. - S
1/4" = 1'-0"

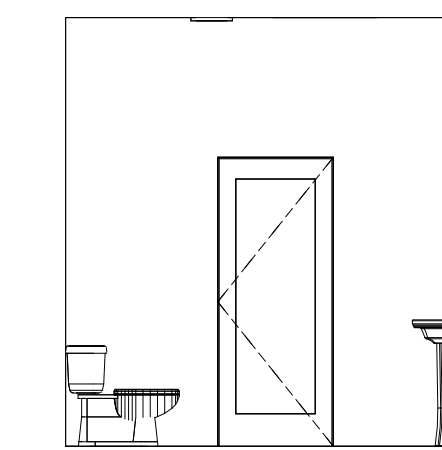


16 P.R. - WEST
1/4" = 1'-0"

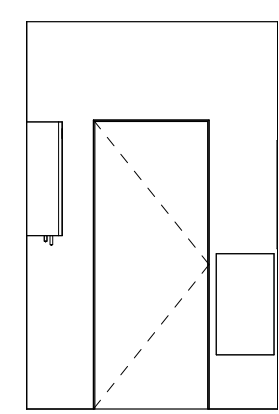


17 UTILITY - NORTH
1/4" = 1'-0"

 


18 UTILITY - EAST
1/4" = 1'-0"

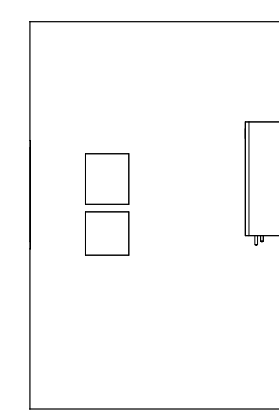


19 UTILITY - SOUTH
1/4" = 1'-0"

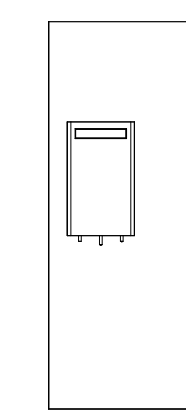


20 UTILITY - WEST
1/4" = 1'-0"

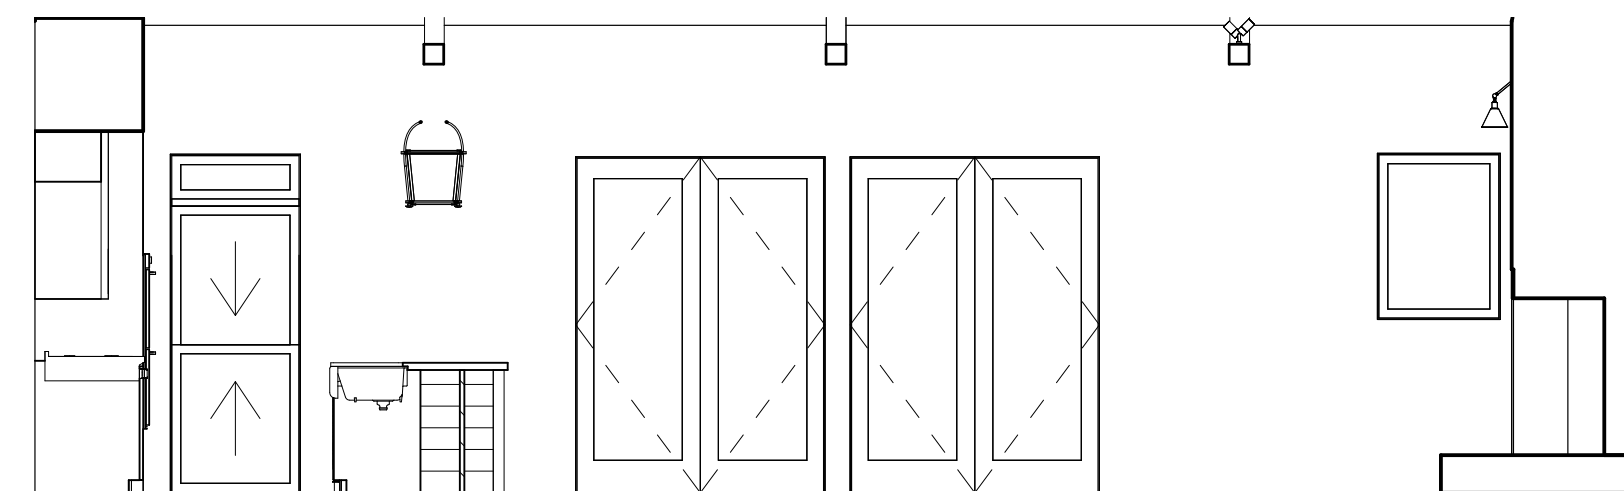


21 KITCHEN - NORTH
1/4" = 1'-0"

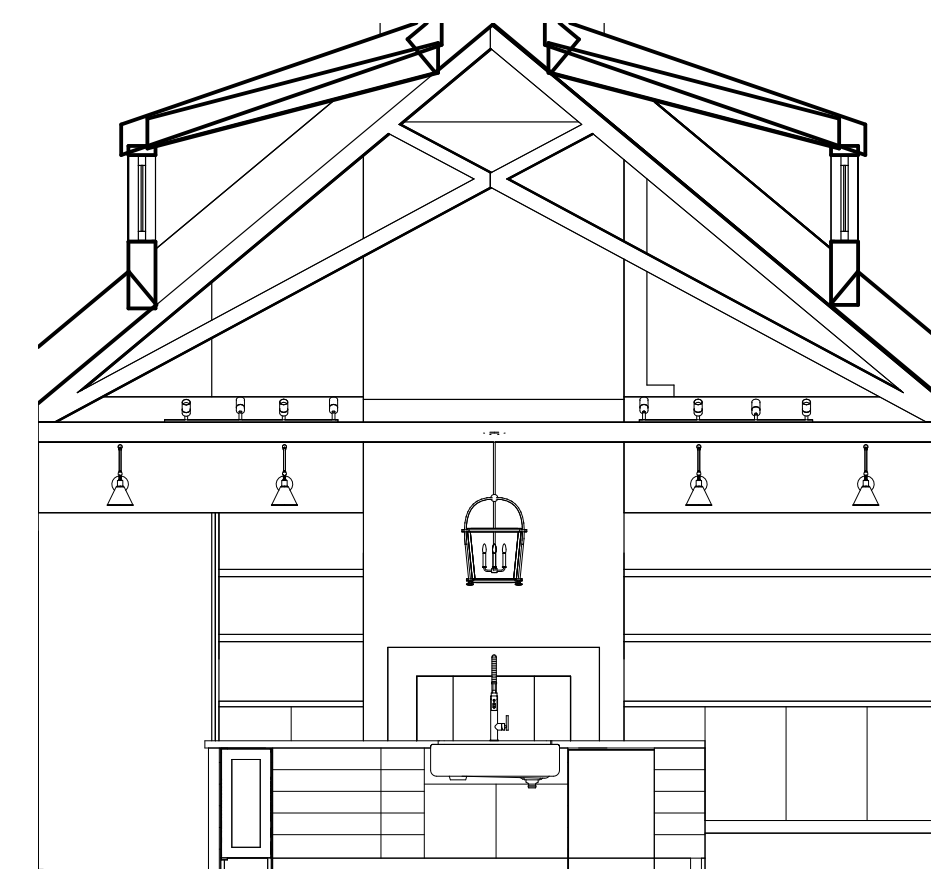


22 KITCHEN - EAST
1/4" = 1'-0"

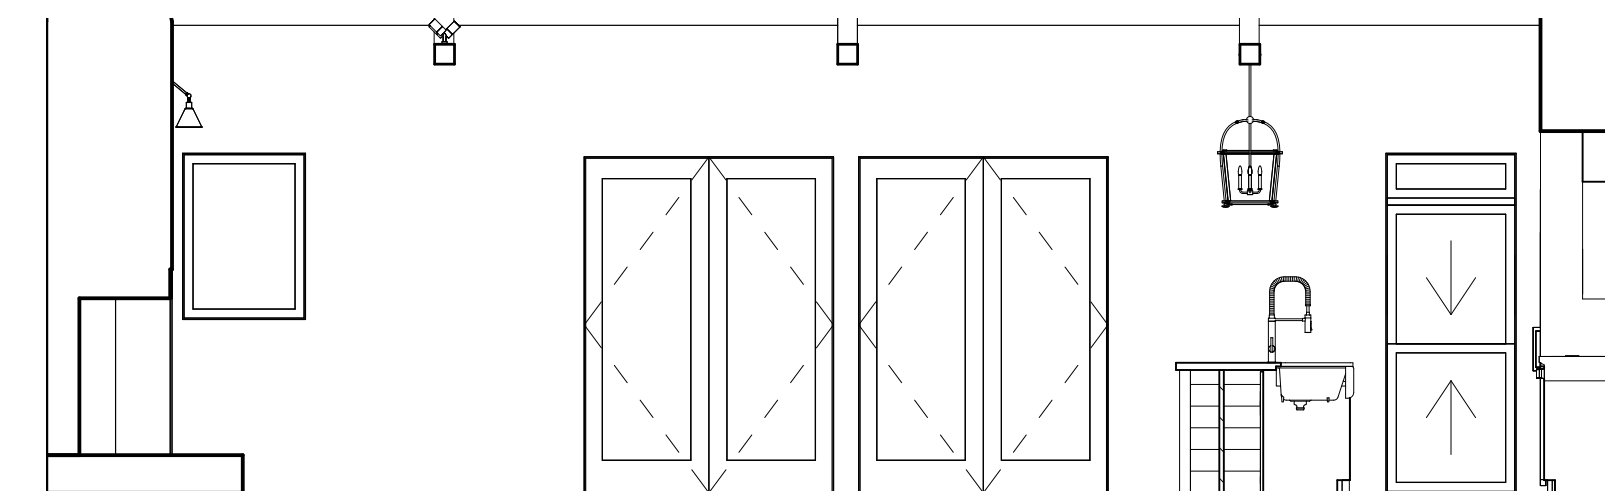


23 KITCHEN - SOUTH
1/4" = 1'-0"

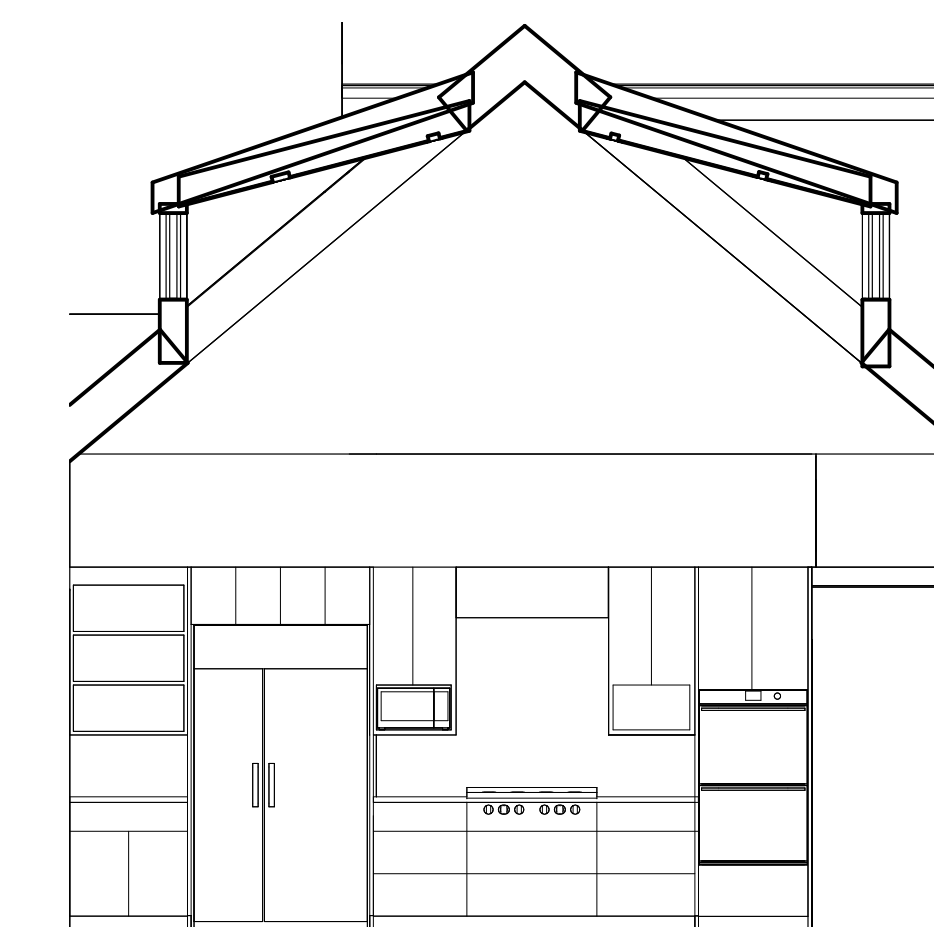


24 KITCHEN - WEST
1/4" = 1'-0"

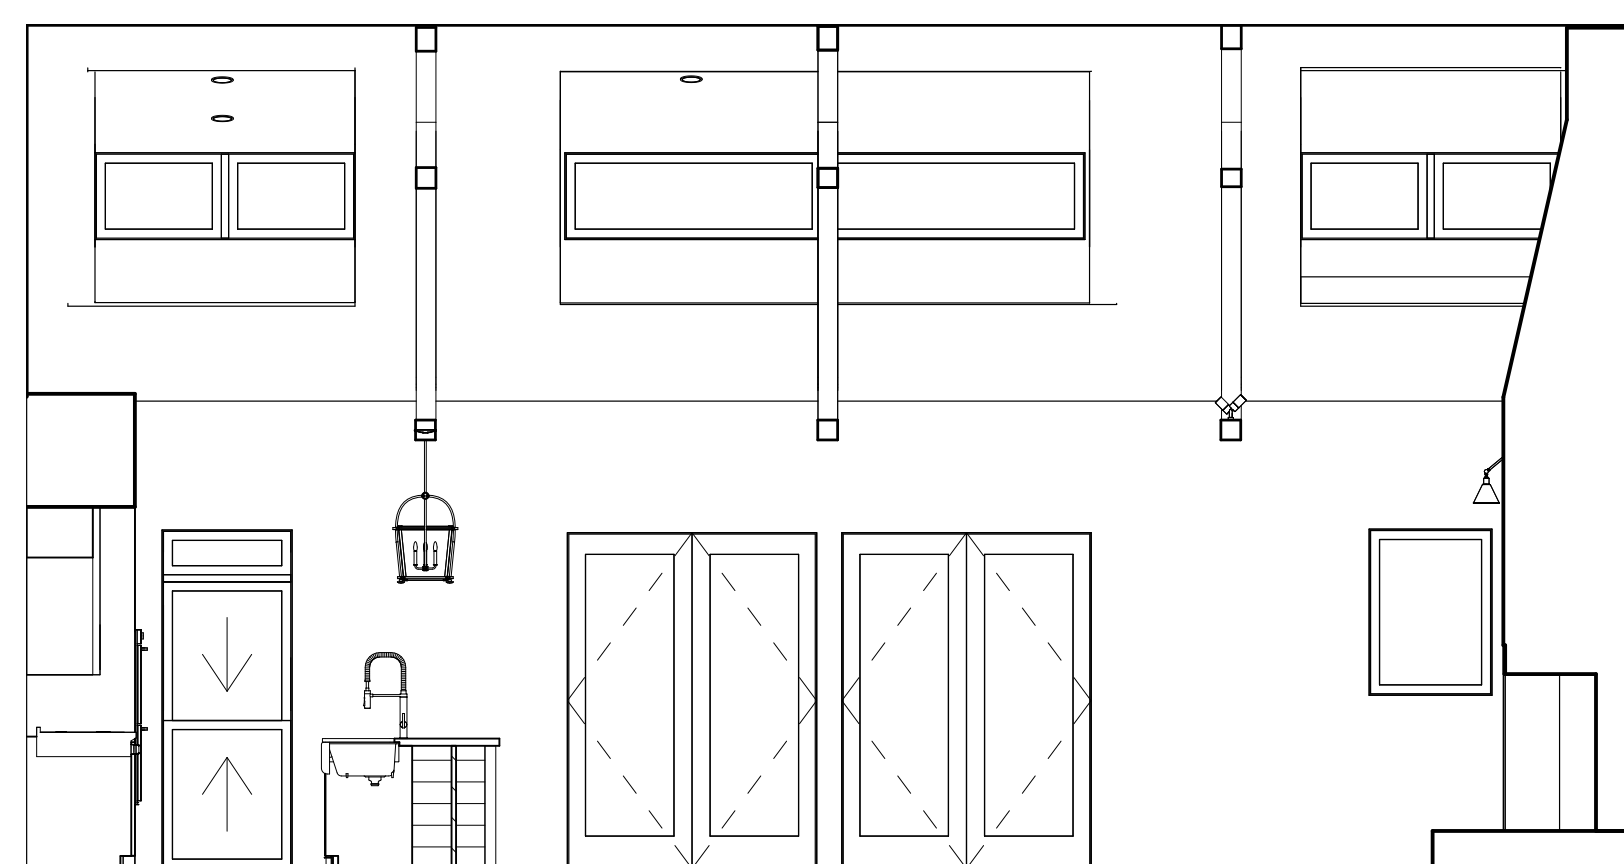


25 GREAT ROOM - NORTH
1/4" = 1'-0"

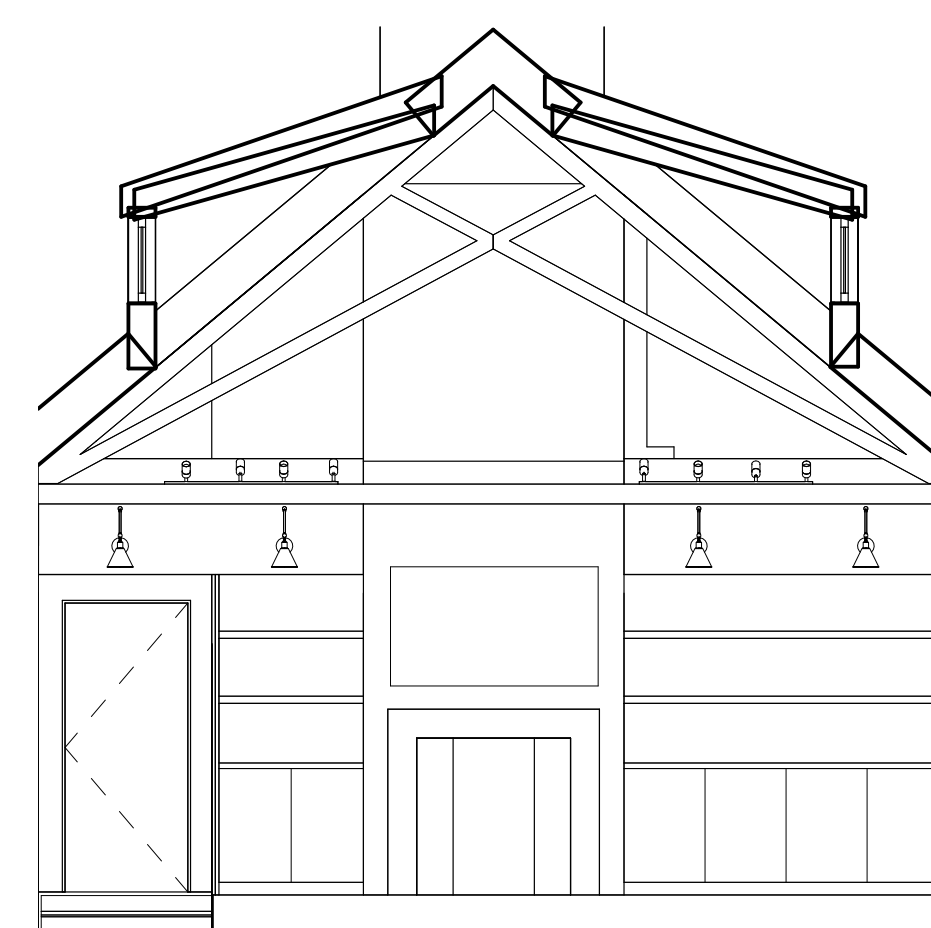


26 GREAT ROOM - EAST
1/4" = 1'-0"

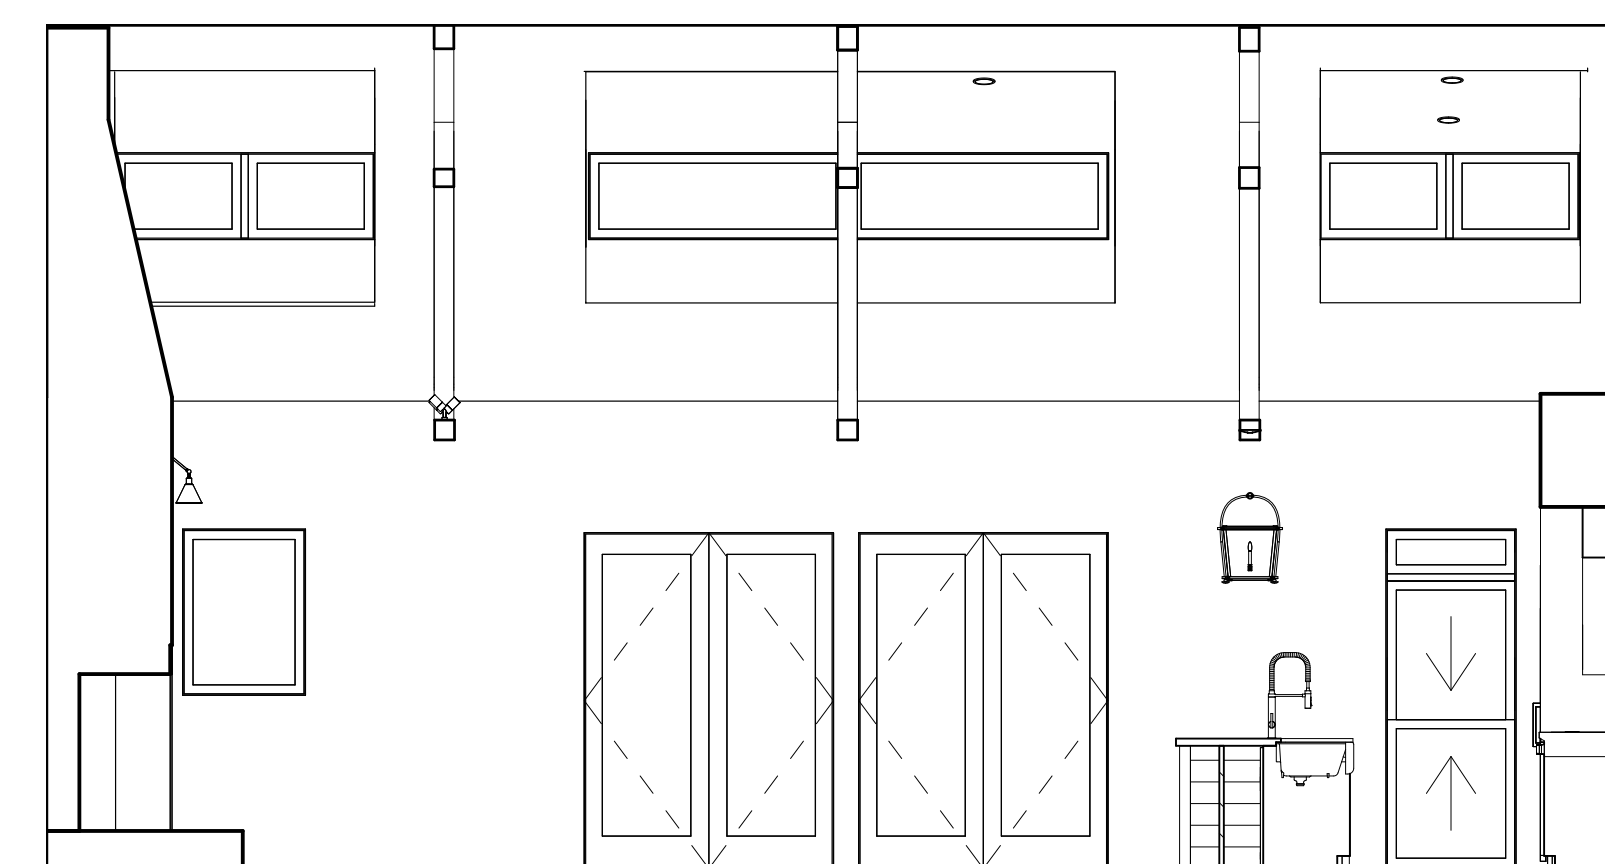


27 GREAT ROOM - SOUTH
1/4" = 1'-0"

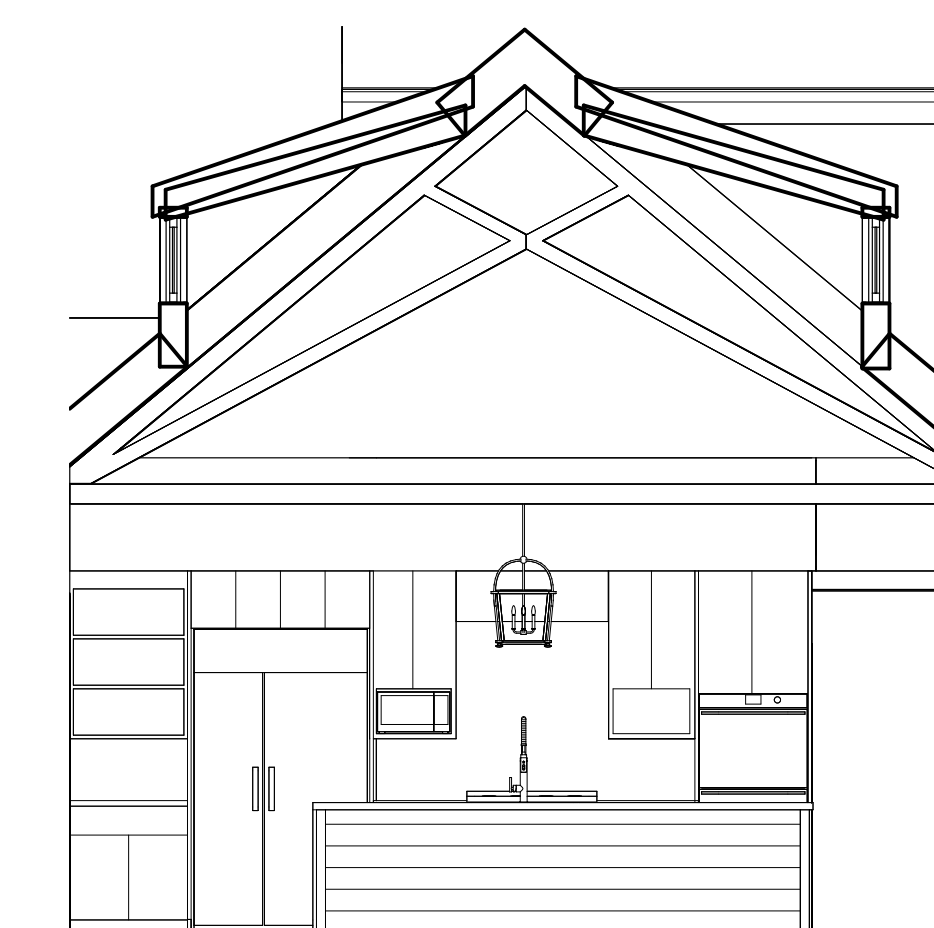


28 GREAT ROOM - WEST
1/4" = 1'-0"

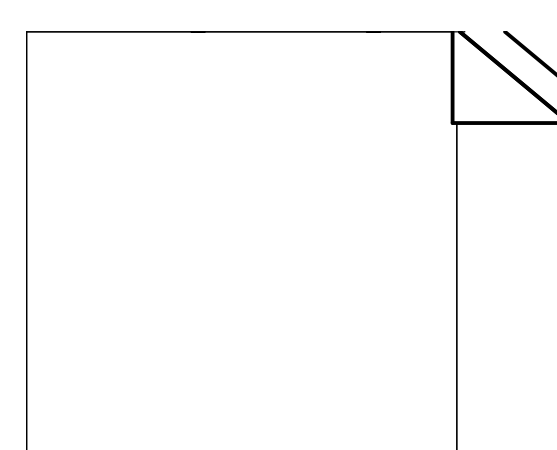


29 FAMILY ROOM - NORTH
1/4" = 1'-0"

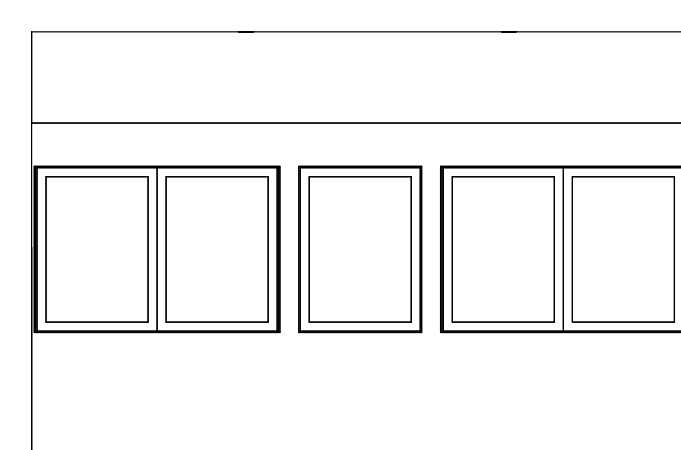


30 FAMILY ROOM - EAST
1/4" = 1'-0"

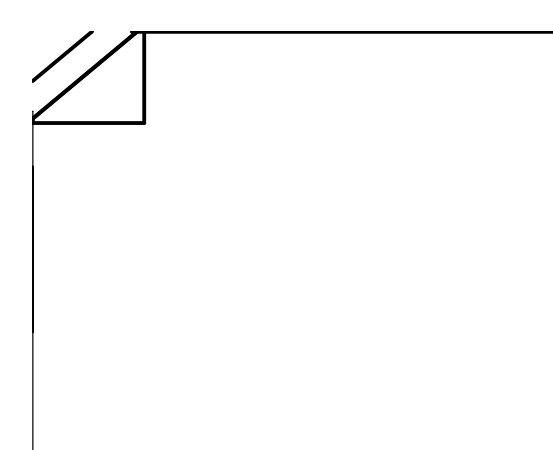


31 FAMILY ROOM - SOUTH
1/4" = 1'-0"

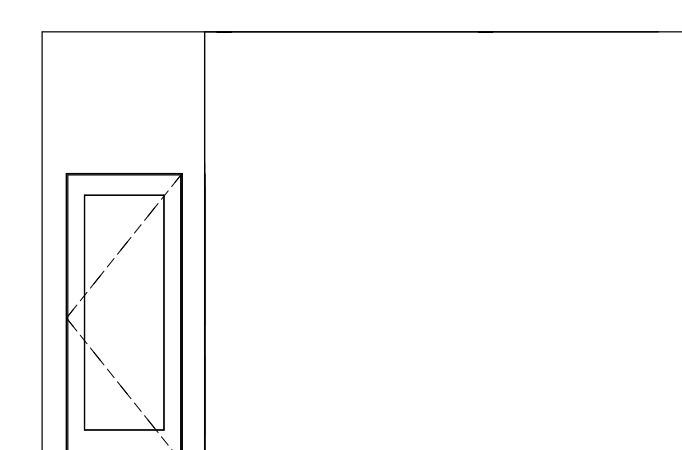


32 FAMILY ROOM - WEST
1/4" = 1'-0"

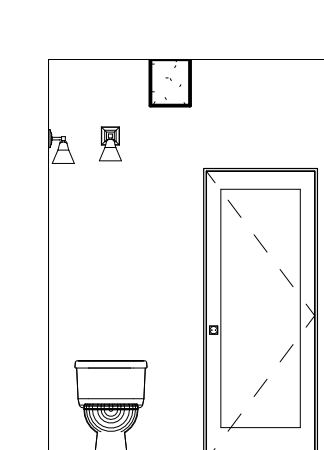


33 GARAGE BATH - NORTH
1/4" = 1'-0"

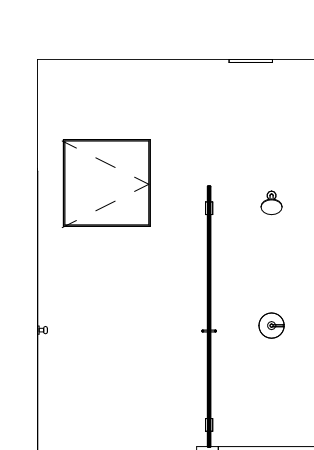

34 GARAGE BATH - EAST
1/4" = 1'-0"

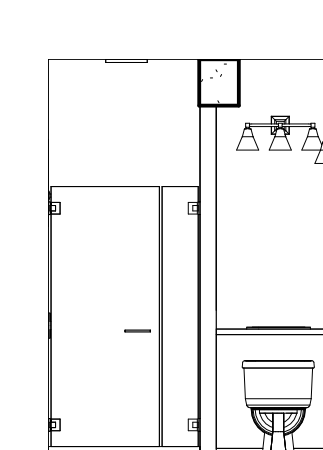

35 GARAGE BATH - SOUTH
1/4" = 1'-0"

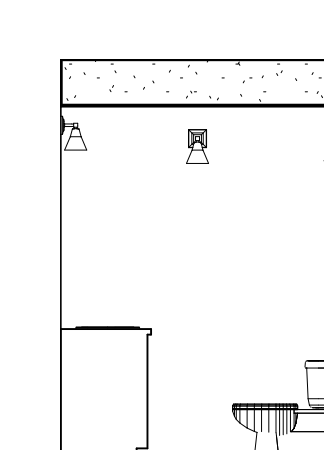

36 GARAGE ELEVATION - WEST
1/4" = 1'-0"



GROUND TRUTH
CAPTURE REALITY AT SCALE

Author

Drawn

Existing Conditions

RESIDENT

XXX

SHEET NO.

A0.400

Scale 1/4" = 1'-0"

INTERIOR ELEVATIONS